
CASA DEL ESTUDIANTE · UNC · PY-2026-055

Cámaras y recorridos de cableado

Nova Domus · Integración Tecnológica

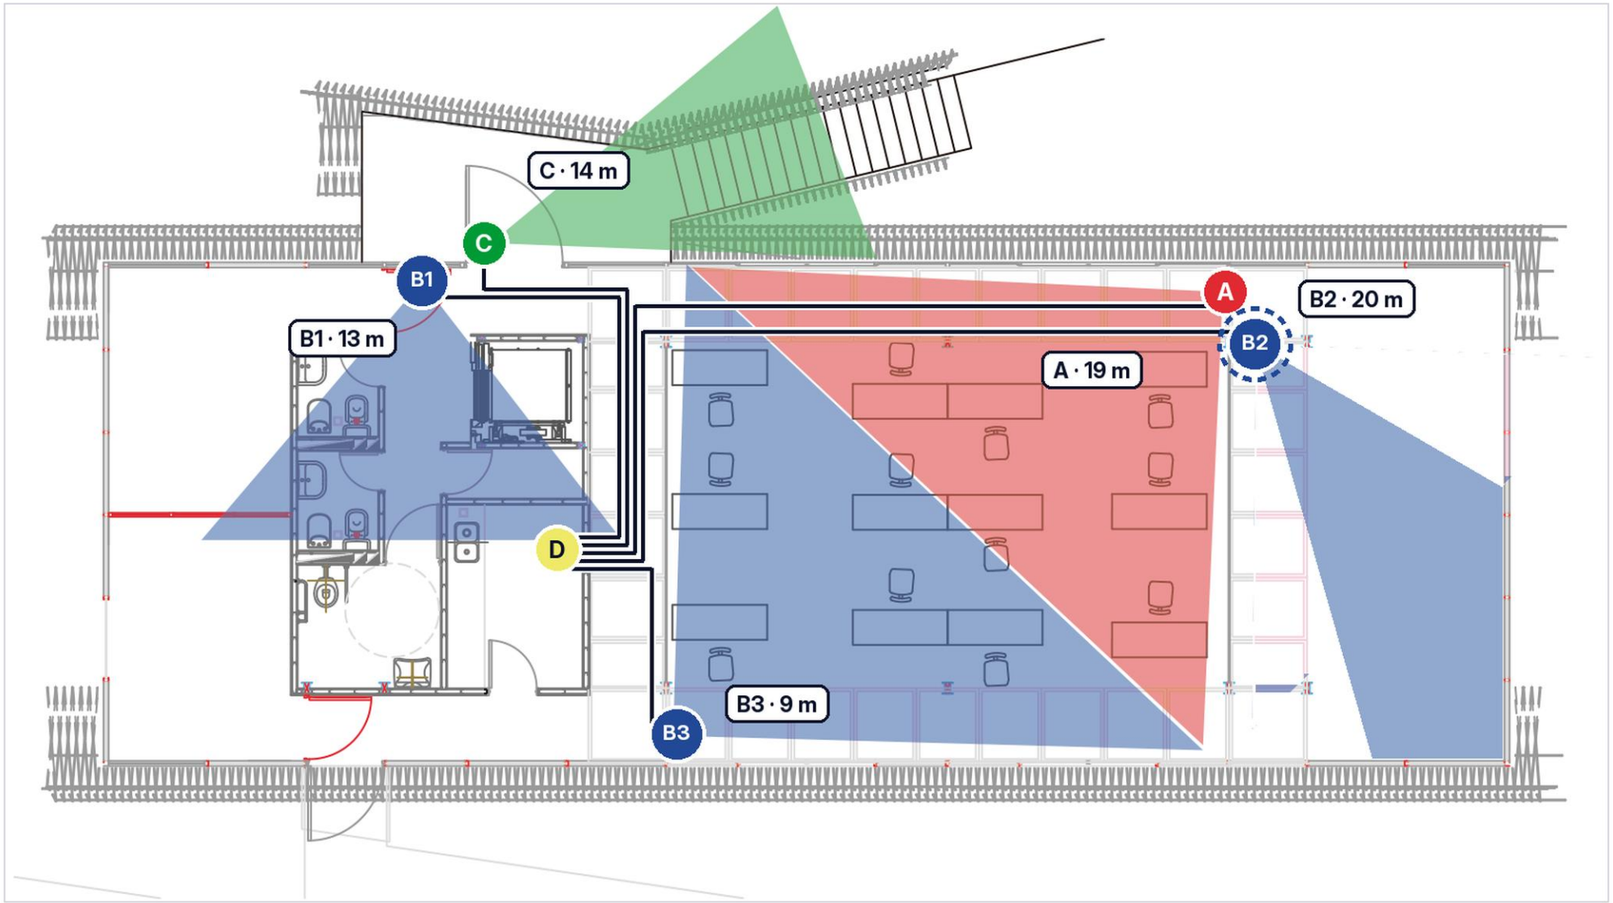

UBICACIÓN DE CÁMARAS Y GRABADOR

Sobre el plano del pliego. Cada letra coincide con el plano y con el detalle de la propuesta.

- **A** — **Turret 4MP AcuSense con audio — Hikvision DS-2CD1347G3-LIUF/SRB.** Reemplaza a la DS-2CD2443G0-IW del pliego, discontinuada.
- **B1** — **Domo 2MP interior — Hikvision DS-2CD1321G0-I. Ingreso.**
- **B2** — **Domo 2MP interior — mismo modelo. Reorientada hacia el interior: en el pliego** miraba hacia afuera del edificio · a confirmar.
- **B3** — **Domo 2MP interior — mismo modelo. Esquina inferior izquierda de la sala.**
- **C** — **Bullet 4MP exterior — Hikvision DS-2CD1043G2-LIUF. Acceso por escalera y puerta** de entrada.
- **D** — **Grabador NVR 8 canales PoE — Hikvision DS-7608NI-Q1/8P. Las 5 cámaras se** conectan a sus puertos PoE.

— Recorrido de cada cable hasta el grabador, en caño semirrígido: por encima del cielorraso (cañería oculta) o fijado a la placa del cielorraso (cañería a la vista), según la opción elegida.

Borde punteado: a confirmar en la visita técnica.

A CARGO DEL ÁREA DE SISTEMAS DE LA UNC

- Configuración del grabador y del software de la PC del Centro de Imágenes.
- Conexión por fibra, rack y UPS.
- Nova Domus instala: cableado, cámaras y grabador, con las cámaras conectadas a los puertos PoE.

RECORRIDO DE CABLEADO — ESTIMADO

A	Turret 4MP — esquina superior derecha de la sala	**19 m**
B2	Domo 2MP — pasillo lateral derecho	**20 m**
C	Bullet 4MP exterior — acceso por escalera (último tramo en cable de exterior)	**14 m**
B1	Domo 2MP — ingreso, junto a la puerta	**13 m**
B3	Domo 2MP — esquina inferior izquierda de la sala	**9 m**
	Medido sobre el plano (5 tiradas, con bajadas y rulos de reserva)	75 m
	Reserva por recorrido real sobre el cielorraso, desvíos de estructura y bajadas	45 m
	Total de cable cotizado	**120 m**

La tirada más larga (20 m) queda muy por debajo del límite de 90 m del cable UTP.

Documento para conversar la propuesta, no es un plano de obra. Base: plano del pliego (sin cotas); escala estimada con el círculo de giro del baño accesible (Ø 1,50 m).

Del cable a la app.