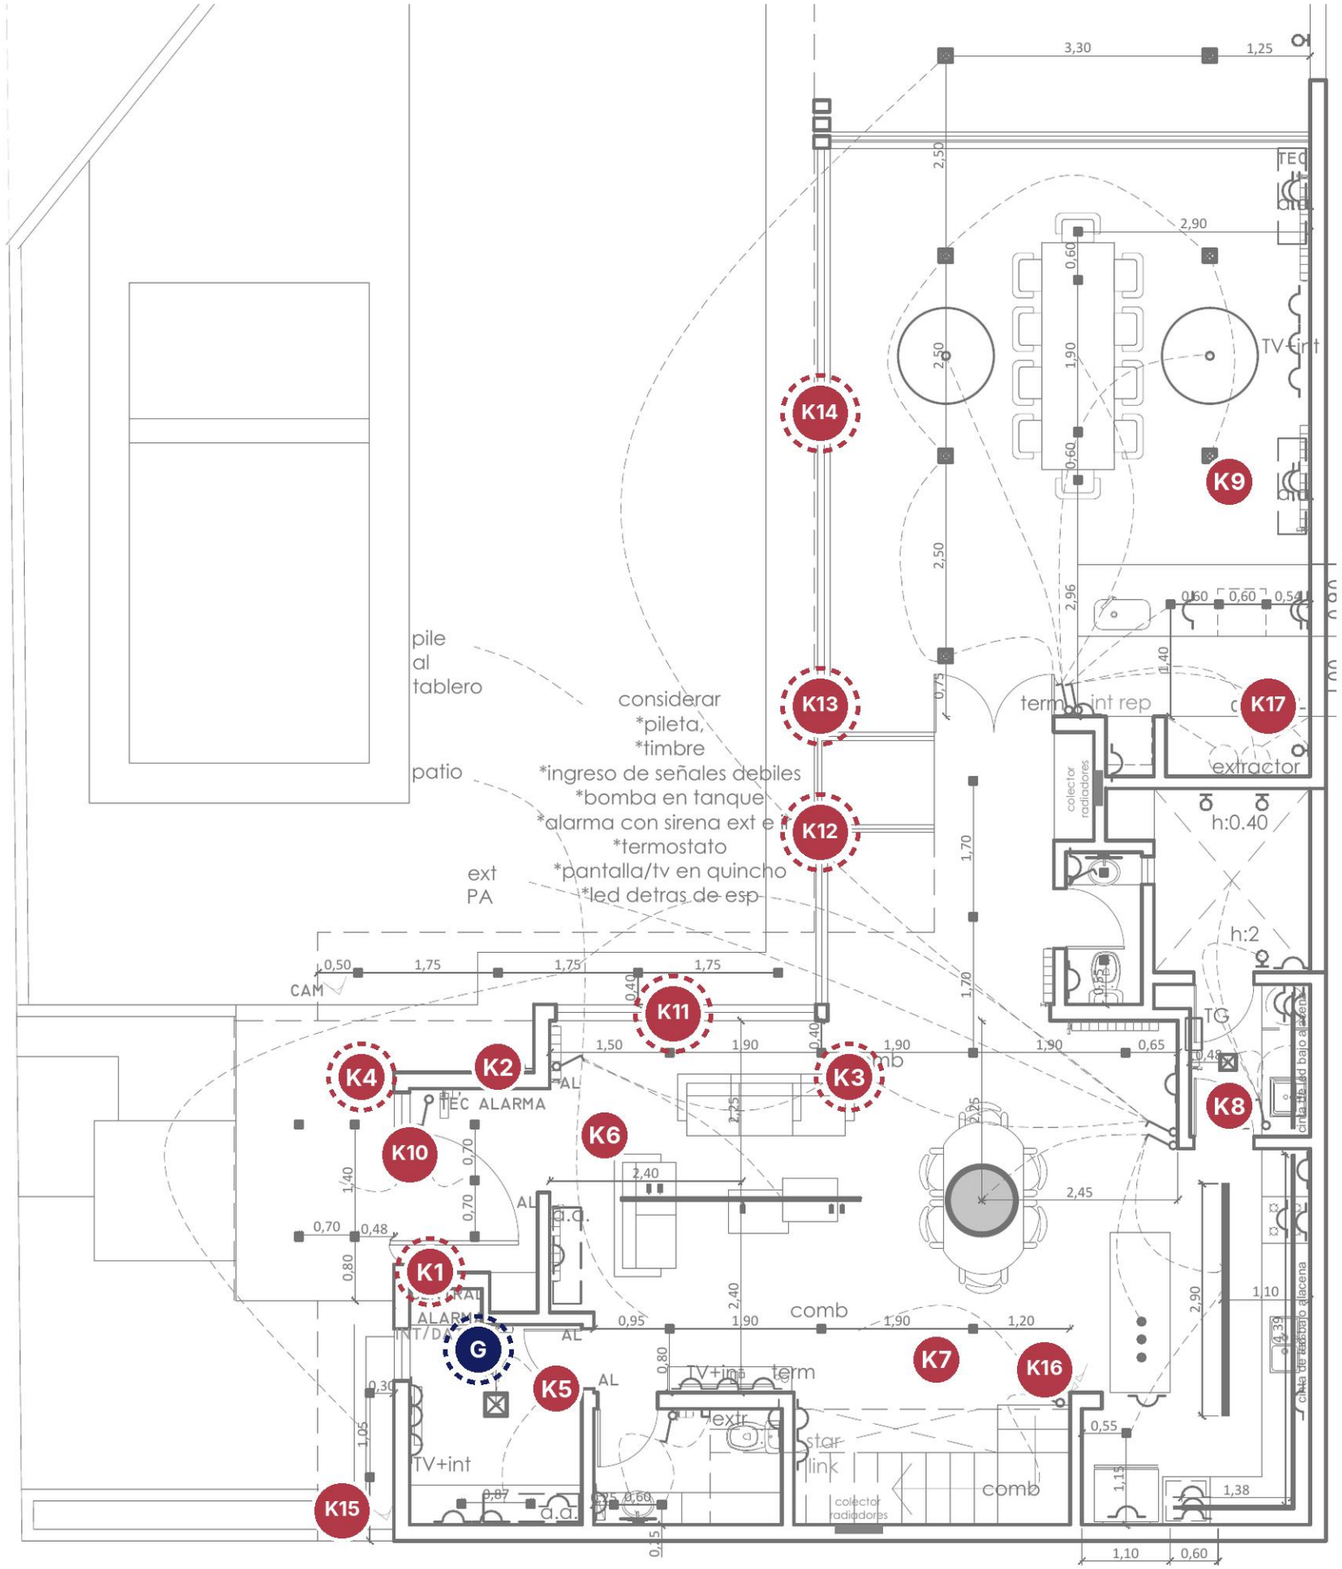


UBICACIÓN PROPUESTA DE DISPOSITIVOS

Dónde proponemos cada dispositivo. Los números de la leyenda coinciden con el plano.

SEGURIDAD Y ACCESOS

- **K1** Central de alarma, junto al rack de la Etapa 1 · a confirmar
- **K2** Teclado — ingreso
- **K3** Sirena interior — estar · a confirmar
- **K4** Sirena exterior — frente · a confirmar
- **K5** Detector de movimiento — estudio
- **K6** Detector de movimiento — ingreso y estar
- **K7** Detector de movimiento — comedor
- **K8** Detector de movimiento — cocina y lavadero
- **K9** Detector de movimiento — galería
- **K10** Contacto magnético — puerta de ingreso
- **K11** Contacto magnético — ventanal del estar · a confirmar
- **K12** Contacto magnético — ventanal de la galería · a confirmar
- **K13** Contacto magnético — ventanal de la galería · a confirmar
- **K14** Contacto magnético — ventanal de la galería · a confirmar
- **K15** Cámara exterior — frente
- **K16** Cámara interior — comedor y escalera
- **K17** Cámara exterior — galería


RED Y CORE

- **G** Rack de la Etapa 1 — grabador de cámaras en bandeja nueva · a confirmar

Borde punteado: ubicación a confirmar en la visita técnica.

PARA EL ELECTRICISTA DE LA OBRA

- Cámaras (K15, K16, K17): caño y cable UTP desde cada una hasta el rack, antes de cerrar paredes.
- La alarma es inalámbrica: detectores, contactos y sirenas no llevan cable.
- Central (K1): tomacorriente cerca del rack.

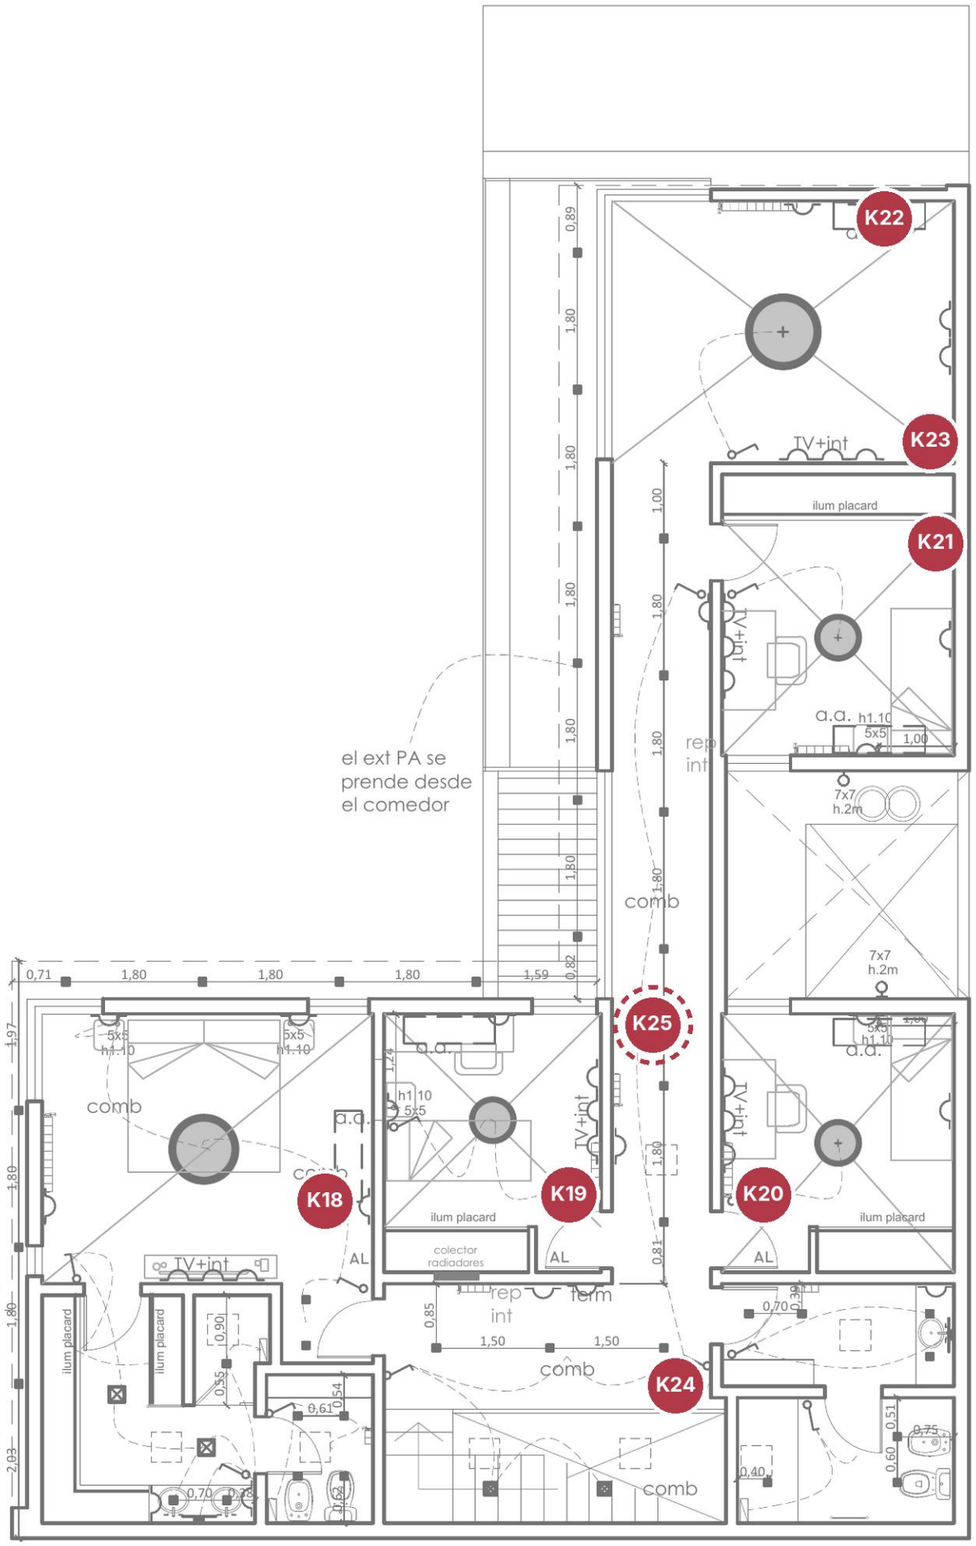

UBICACIÓN PROPUESTA DE DISPOSITIVOS

Dónde proponemos cada dispositivo. Los números de la leyenda coinciden con el plano.

SEGURIDAD Y ACCESOS

- **K18** Detector de movimiento — dormitorio principal
- **K19** Detector de movimiento — dormitorio
- **K20** Detector de movimiento — dormitorio
- **K21** Detector de movimiento — dormitorio
- **K22** Detector de movimiento — gimnasio
- **K23** Cámara interior — gimnasio
- **K24** Cámara interior — hall de planta alta
- **K25** Repetidor de la alarma — hall de planta alta · a confirmar

Borde punteado: ubicación a confirmar en la visita técnica.

PARA EL ELECTRICISTA DE LA OBRA

- Cámaras (K23, K24): caño y cable UTP desde cada una hasta el rack de planta baja.
- Repetidor (K25): tomacorriente en el hall; la ubicación se confirma con una prueba de señal.