
# CASA DEL ESTUDIANTE · UNC · PY-2026-055

## Cámaras y recorridos de cableado

Nova Domus · Integración Tecnológica

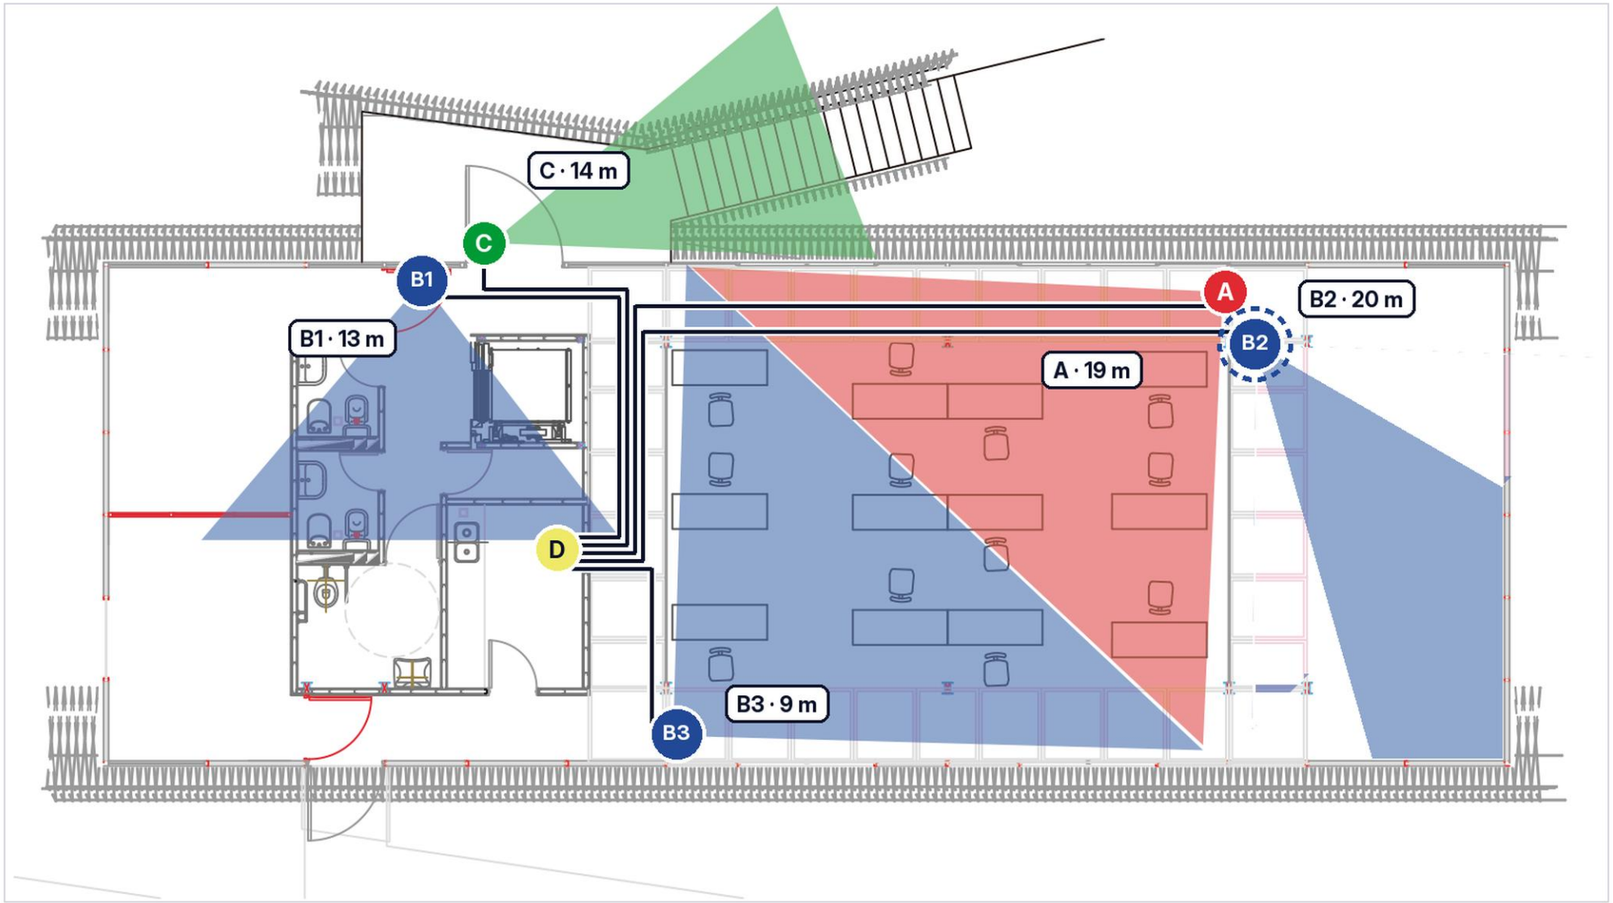


## UBICACIÓN DE CÁMARAS Y GRABADOR

Sobre el plano del pliego. Cada letra coincide con el plano y con el detalle de la propuesta.

- **A** — **Turret 4MP con audio bidireccional y detección de personas — Hikvision** DS-2CD3341G2-LIUF. Reemplaza a la DS-2CD2443G0-IW del pliego, discontinuada.
- **B1** — **Domo 2MP interior — Hikvision DS-2CD1321G0-I (según pliego) o DS-2CD1121G0-I** (opción económica). Ingreso.
- **B2** — **Domo 2MP interior — mismo modelo. Reorientada hacia el interior: en el pliego** miraba hacia afuera del edificio · a confirmar.
- **B3** — **Domo 2MP interior — mismo modelo. Esquina inferior izquierda de la sala.**
- **C** — **Bullet 4MP exterior — Hikvision DS-2CD1043G2-LIUF. Acceso por escalera y puerta** de entrada.
- **D** — **Grabador NVR 8 canales PoE — Hikvision DS-7608NI-Q1/8P. Las 5 cámaras quedan** conectadas a sus puertos PoE.

— Recorrido de cada cable hasta el grabador, en caño semirrígido: por encima del cielorraso (cañería oculta) o fijado a la placa del cielorraso (cañería a la vista), según la opción elegida.

Borde punteado: a confirmar en la visita técnica.

### A CARGO DEL ÁREA DE SISTEMAS DE LA UNC

- Configuración del grabador y del software de la PC del Centro de Imágenes.
- Instalación del grabador en el rack; conexión por fibra, rack y UPS.
- Nova Domus instala: cañería con el cableado y las cámaras, conectadas a los puertos PoE del grabador.

## RECORRIDO DE CABLEADO — ESTIMADO

| | | |
|---|---|---|
| A | Turret 4MP — esquina superior derecha de la sala | **19 m** |
| B2 | Domo 2MP — pasillo lateral derecho | **20 m** |
| C | Bullet 4MP exterior — acceso por escalera (último tramo en cable de exterior) | **14 m** |
| B1 | Domo 2MP — ingreso, junto a la puerta | **13 m** |
| B3 | Domo 2MP — esquina inferior izquierda de la sala | **9 m** |
| | Medido sobre el plano (5 tiradas, con bajadas y rulos de reserva) | 75 m |
| | Reserva por recorrido real sobre el cielorraso, desvíos de estructura y bajadas | 45 m |
| | **Total de cable cotizado** | **120 m** |

La tirada más larga (20 m) queda muy por debajo del límite de 90 m del cable UTP.