
VIVIENDA GONZALO · PY-2026-053

Planta baja

Nova Domus · Integración Tecnológica

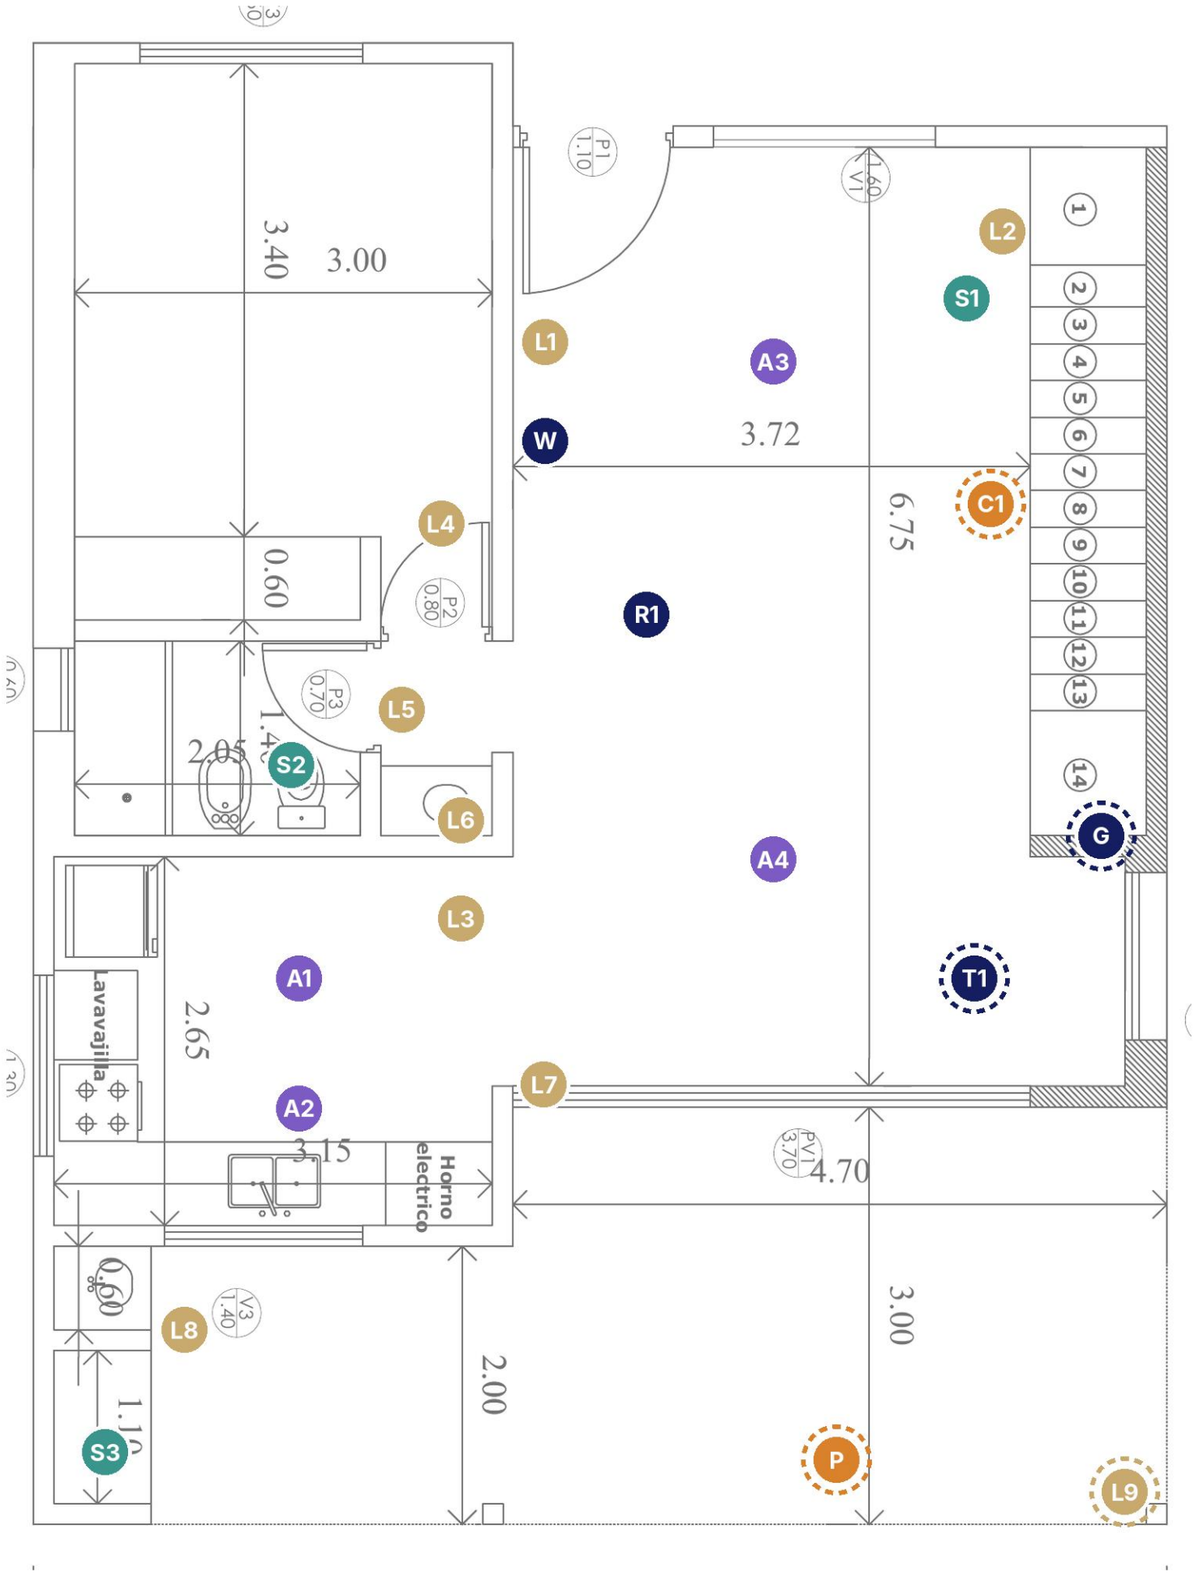

UBICACIÓN PROPUESTA DE DISPOSITIVOS

Dónde proponemos cada dispositivo. Los números de la leyenda coinciden con el plano.

ILUMINACIÓN

- **L1** Llave del ingreso — gargantas del living y del comedor (tiras 24V) + colgante del comedor (Shelly Dimmer en la caja)
- **L2** Escalera — tira LED 24V
- **L3** Cocina — garganta y bajo alacena (24V) + luz general (Shelly 1PM Mini)
- **L4** Dormitorio — 2 efectos de luz indirecta (24V)
- **L5** Baño — luz general (Shelly 1PM Mini) + espejo (24V)
- **L6** Nicho del lavatorio — espejo (24V)
- **L7** Galería — garganta (24V) + luz general (Shelly 1PM Mini)
- **L8** Lavadero — luz general (Shelly 1PM Mini)
- **L9** Parque — luz de parque (Shelly 1PM Mini). Fuera del plano · a confirmar

SENSORES DE AUTOMATIZACIÓN

- **S1** Escalera — sensor de movimiento
- **S2** Baño — sensores de movimiento y de puerta
- **S3** Lavadero — sensores de movimiento y de puerta

MÚSICA

- **A1** Cocina — parlante embutido en el cielorraso
- **A2** Cocina — parlante embutido en el cielorraso
- **A3** Living — parlante embutido en el cielorraso
- **A4** Comedor — parlante embutido en el cielorraso

RED Y CORE

- **R1** Access point WiFi de planta baja (techo)
- **W** Pantalla de control (Shelly Wall Display) — ingreso principal
- **G** Gabinete de red — router, switch, controlador, servidor Home Assistant, amplificador de música y UPS · a confirmar
- **T1** Tablero de planta baja + caja de control de las tiras LED (3 módulos) · a confirmar


CONFORT Y EXTERIOR

- **C1** Aire acondicionado con Sensibo — ubicación del split · a confirmar
- **P** Pileta y riego — en el tablero de la pileta: bomba + luz (Shelly Pro 2PM), bomba de riego y 4 zonas. Fuera del plano · a confirmar

Borde punteado: ubicación a confirmar en la visita técnica.

PARA EL ELECTRICISTA DE LA OBRA

- Toda caja de llave (L): neutro junto con el retorno.
- Llaves de luz indirecta: retorno hasta la caja T1, en caño aparte del de 220V.
- Cada parlante (A): un caño desde el gabinete G.
- Access point (R1) y pantalla (W): caño + cable de red desde G.
- Bombas de pileta y riego (P): corrugado generoso desde el tablero.

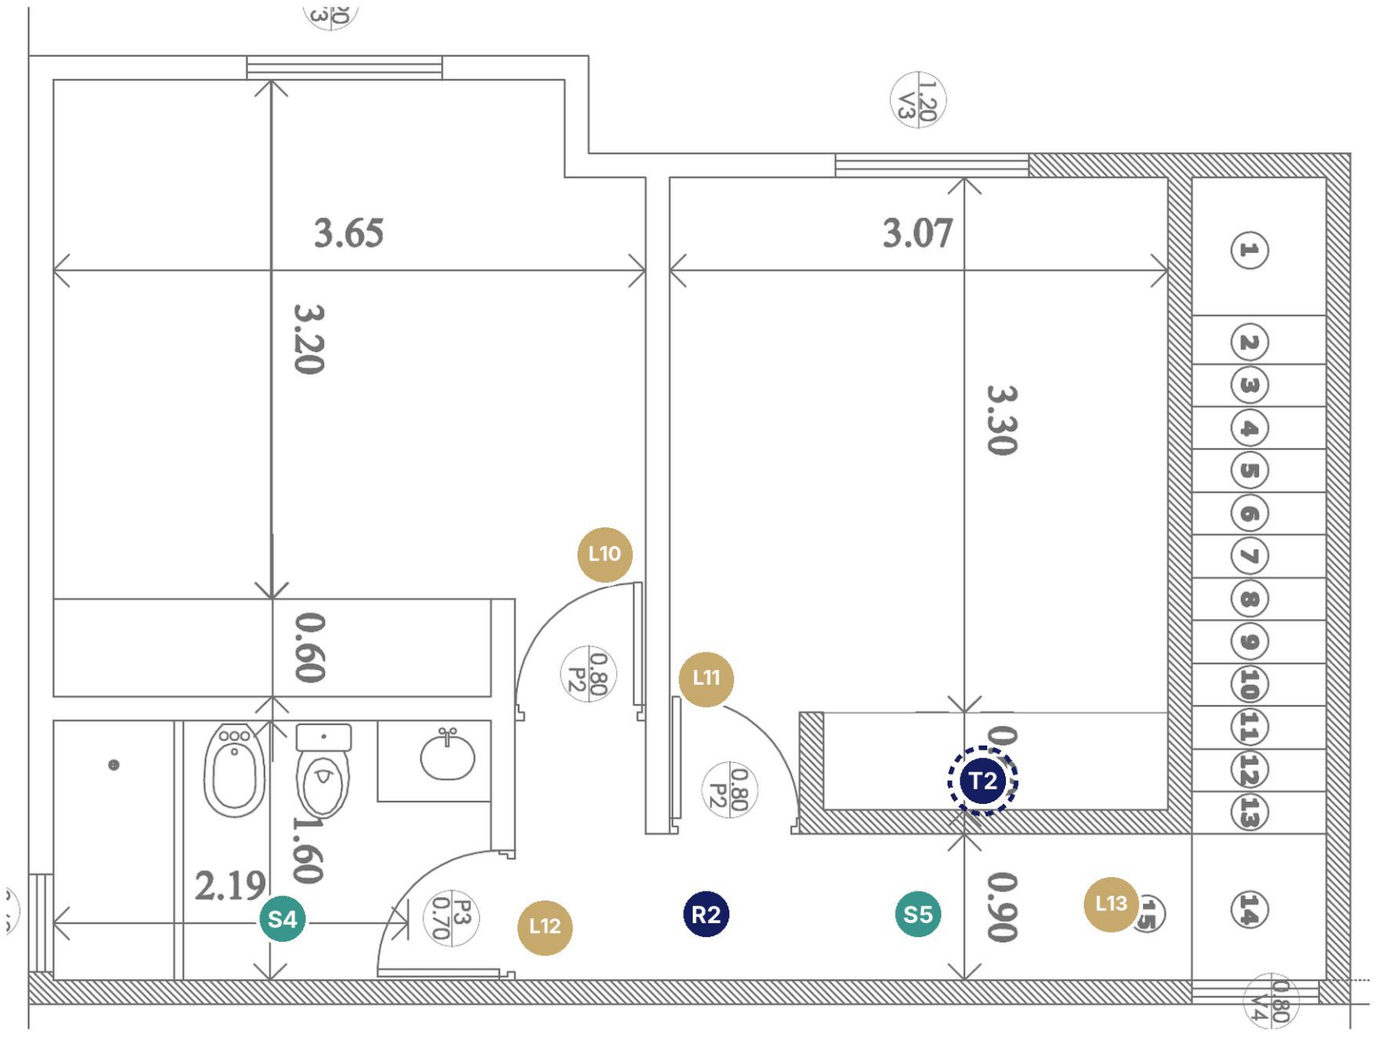

UBICACIÓN PROPUESTA DE DISPOSITIVOS

Dónde proponemos cada dispositivo. Los números de la leyenda coinciden con el plano.

ILUMINACIÓN

- **L10** — Dormitorio 1 — 2 efectos de luz indirecta (24V)
- **L11** — Dormitorio 2 — 2 efectos de luz indirecta (24V)
- **L12** — Baño — luz general (Shelly 1PM Mini) + espejo (24V)
- **L13** — Pasillo y llegada de la escalera — tira LED 24V

SENSORES DE AUTOMATIZACIÓN

- **S4** — Baño — sensores de movimiento y de puerta
- **S5** — Pasillo — sensor de movimiento

RED Y CORE

- **R2** — Access point WiFi de planta alta (techo)
- **T2** — Caja de control de las tiras LED de planta alta (2 módulos) — en placard o junto al tablero seccional · a confirmar

Borde punteado: ubicación a confirmar en la visita técnica.

PARA EL ELECTRICISTA DE LA OBRA

- Toda caja de llave (L): neutro junto con el retorno.
- Llaves de luz indirecta: retorno hasta la caja T2, en caño aparte del de 220V.
- Access point (R2): caño + cable de red desde el gabinete G (planta baja).