



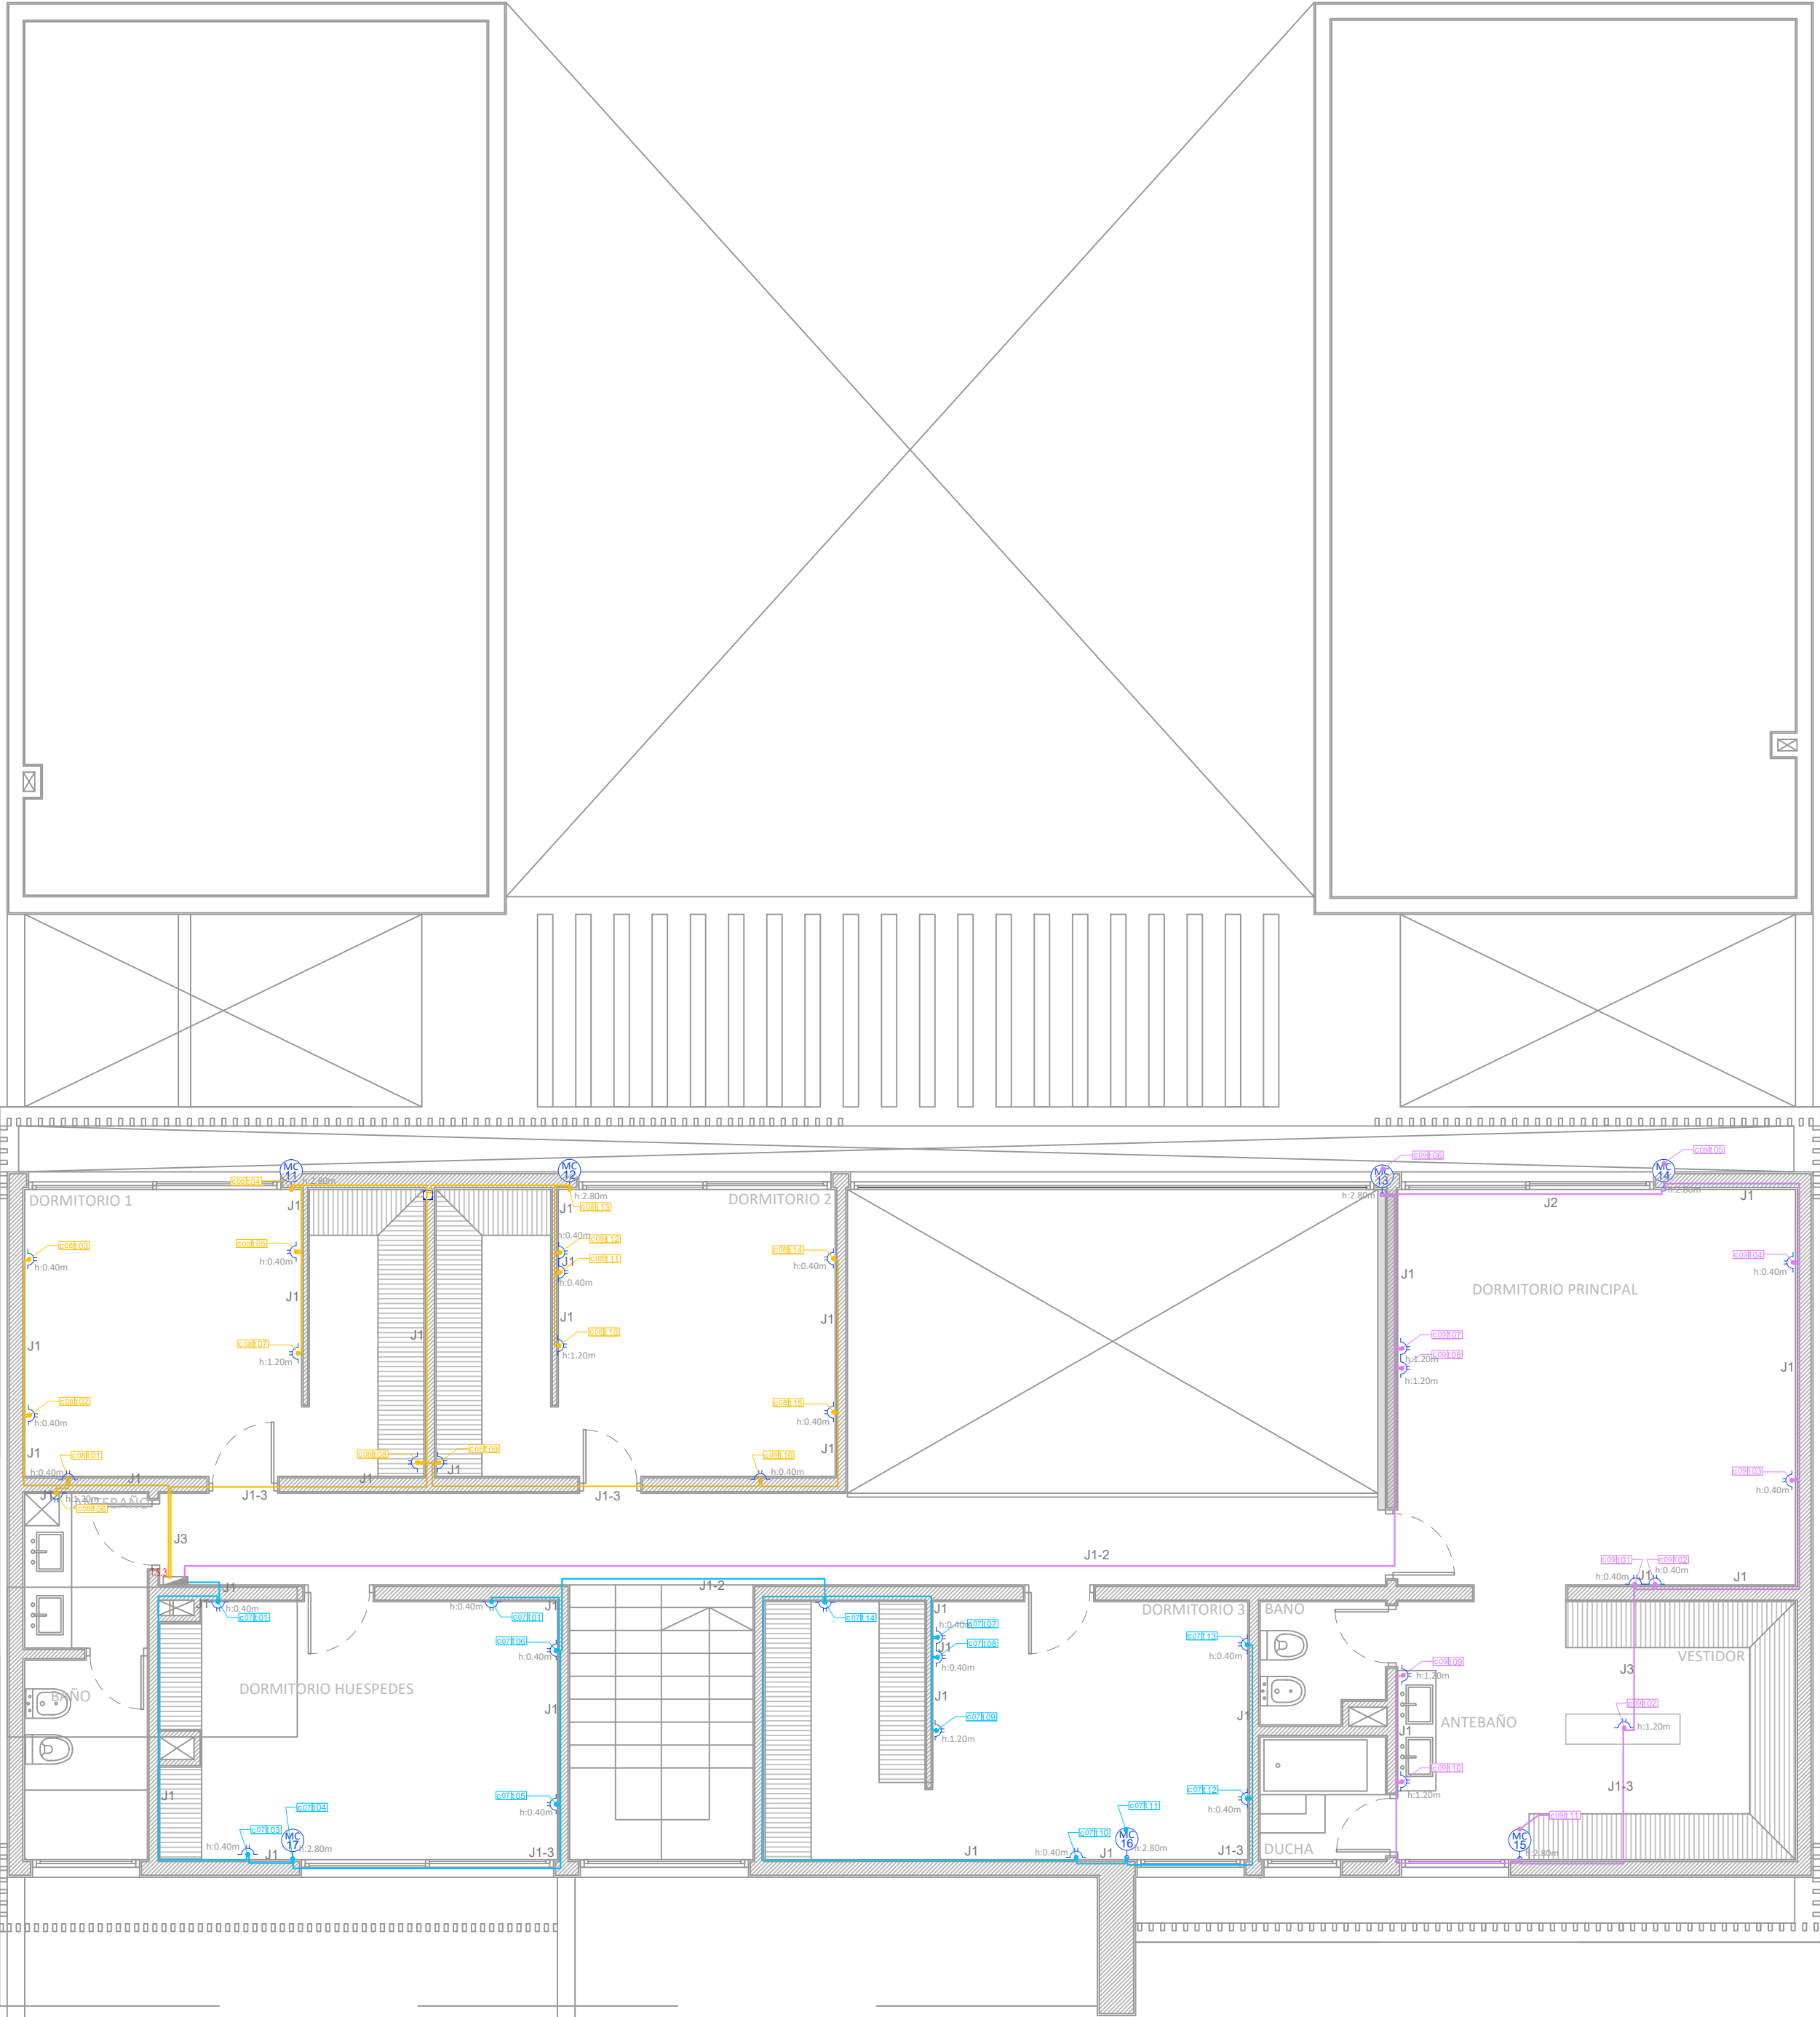


Estudio jad - Casa JB - Campos del virrey

PLANTA BAJA - TUG y CORTINEROS

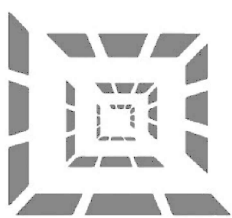

REFERENCIAS

ELECTRICIDAD

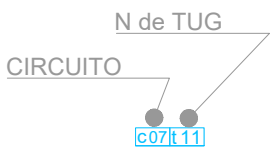

	Toma Simple 10A
	Toma doble 10A
	Toma doble 10A capsulado
	Extractor de aire
	Caja estanca 10x10
	Toma Simple 20A
	Motor cortienro