
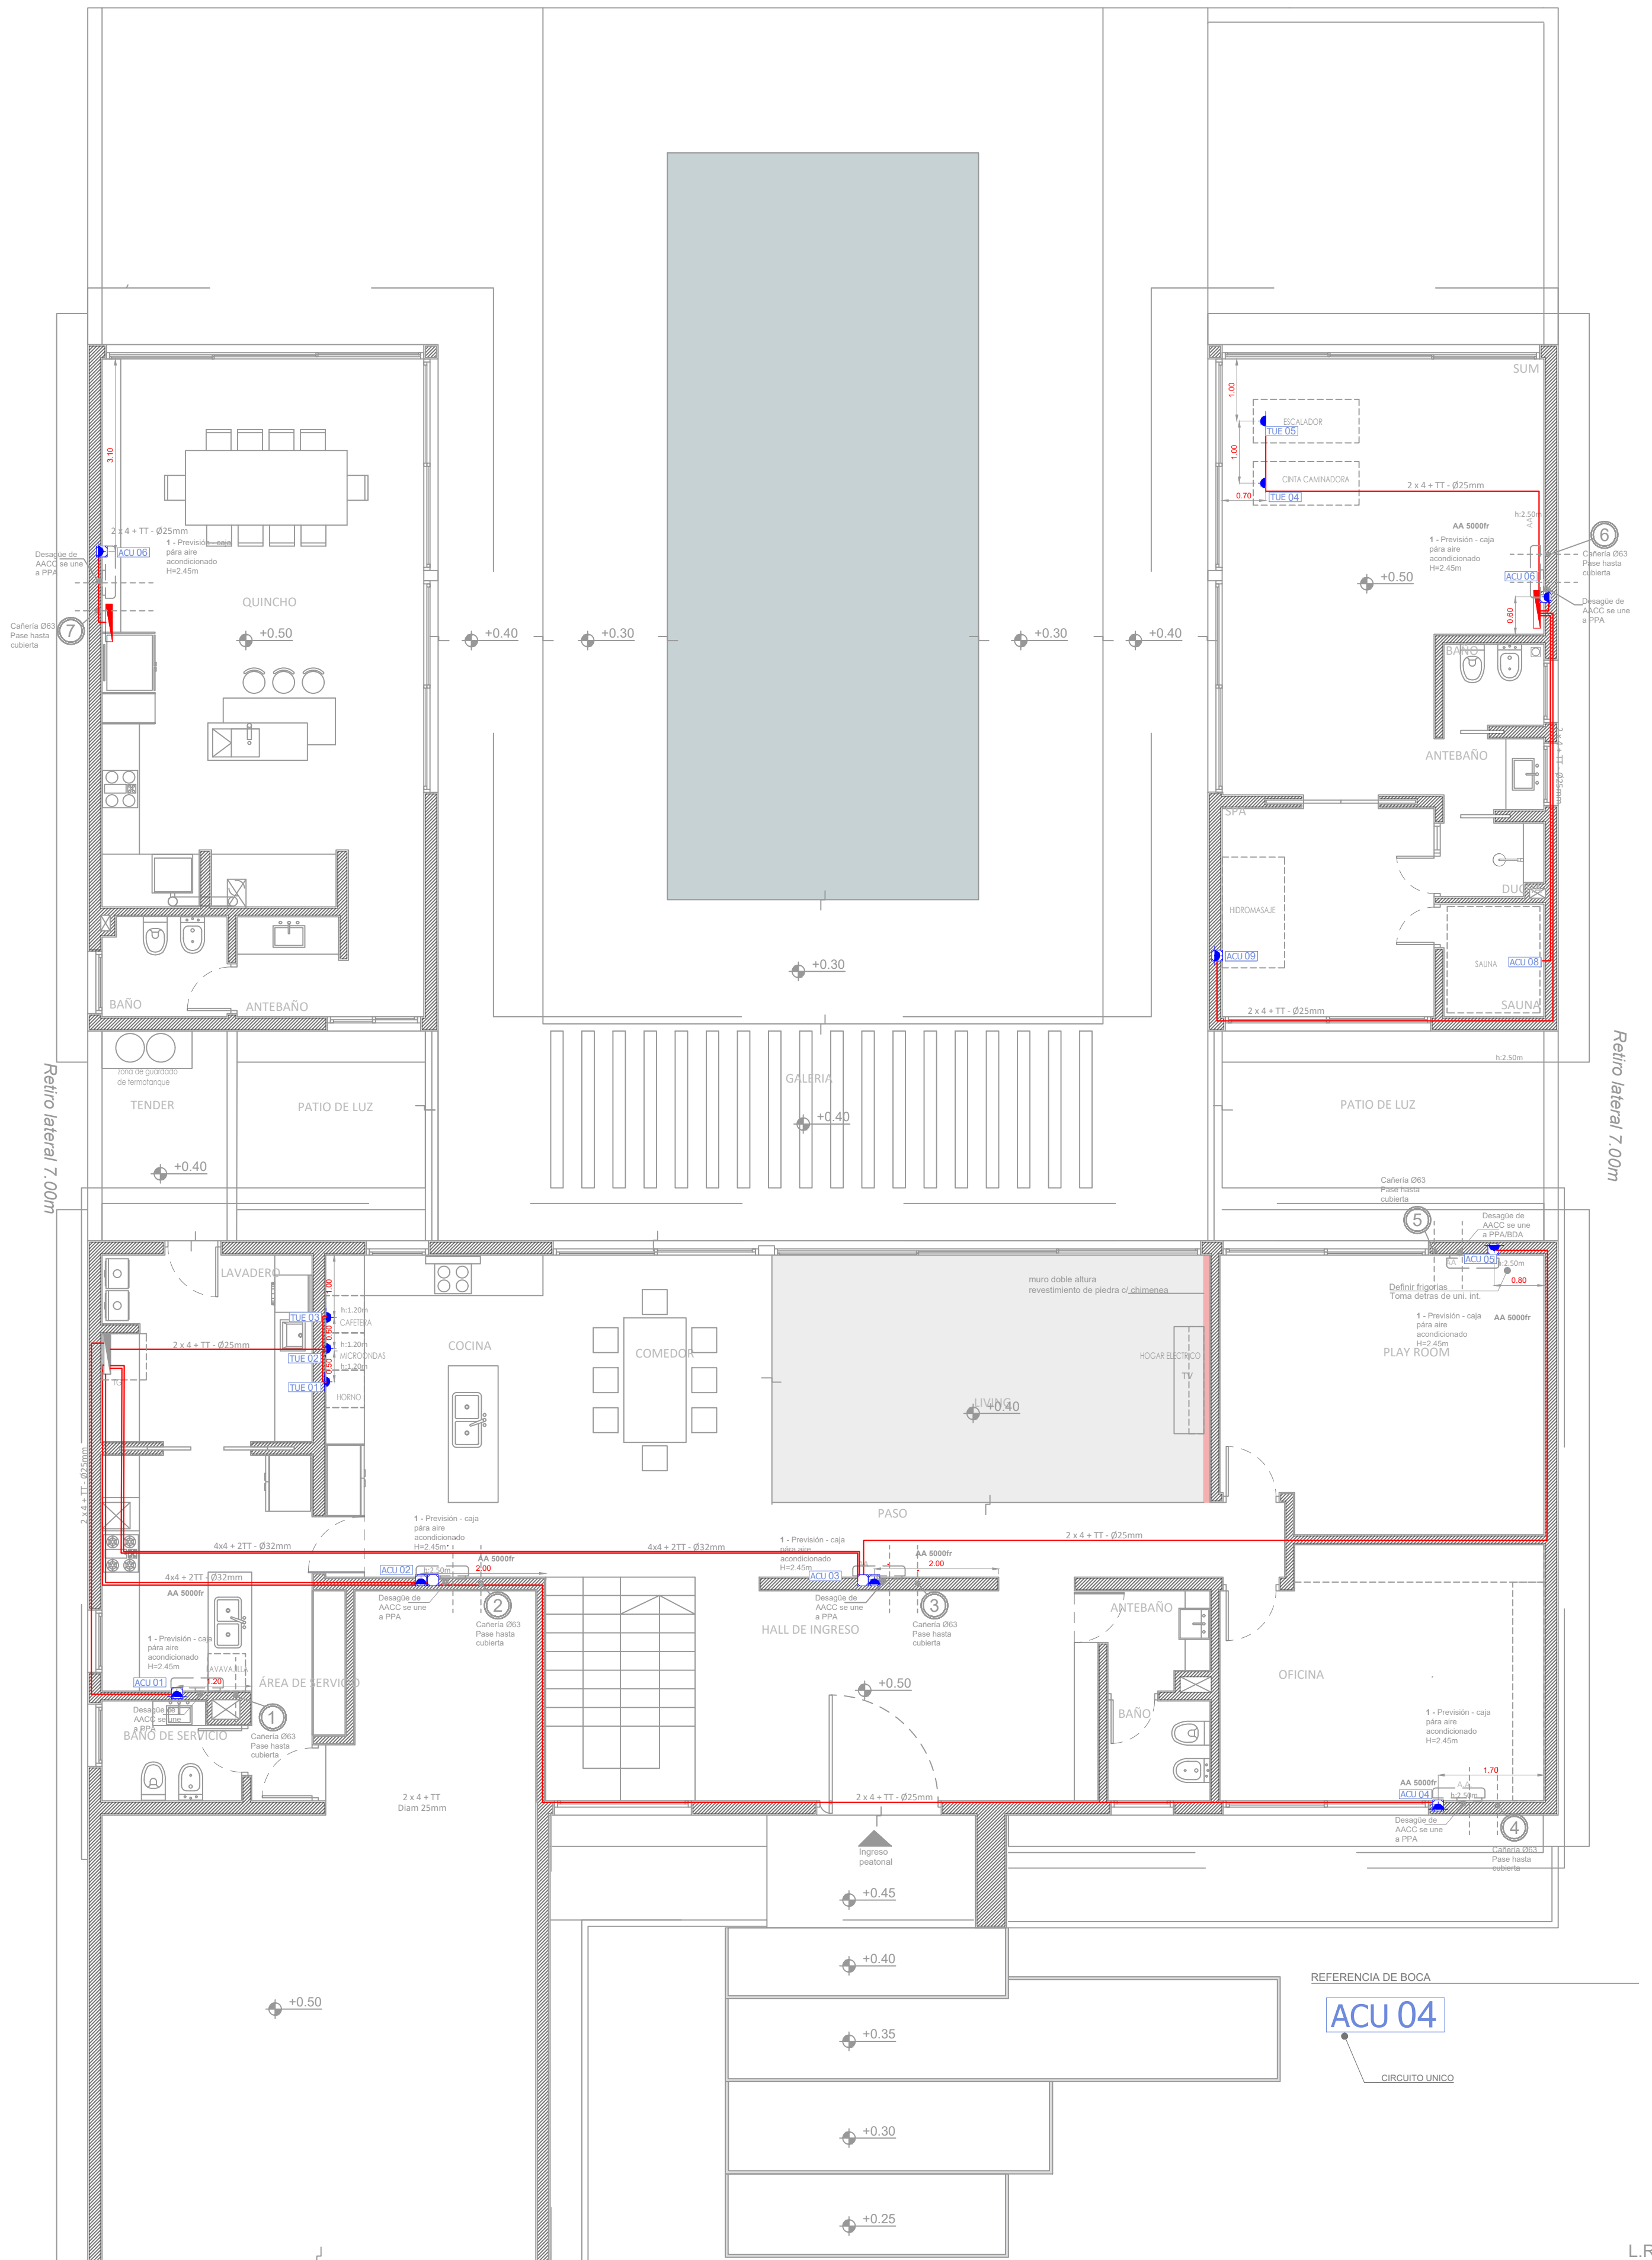




Estudio jad - Casa JB - Campos del virrey

PLANTA BAJA - ACU y TUE

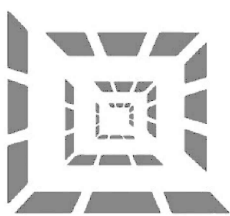

Estudio jad - Casa JB - Campos del virrey


PLANTA BAJA - ACU y TUE

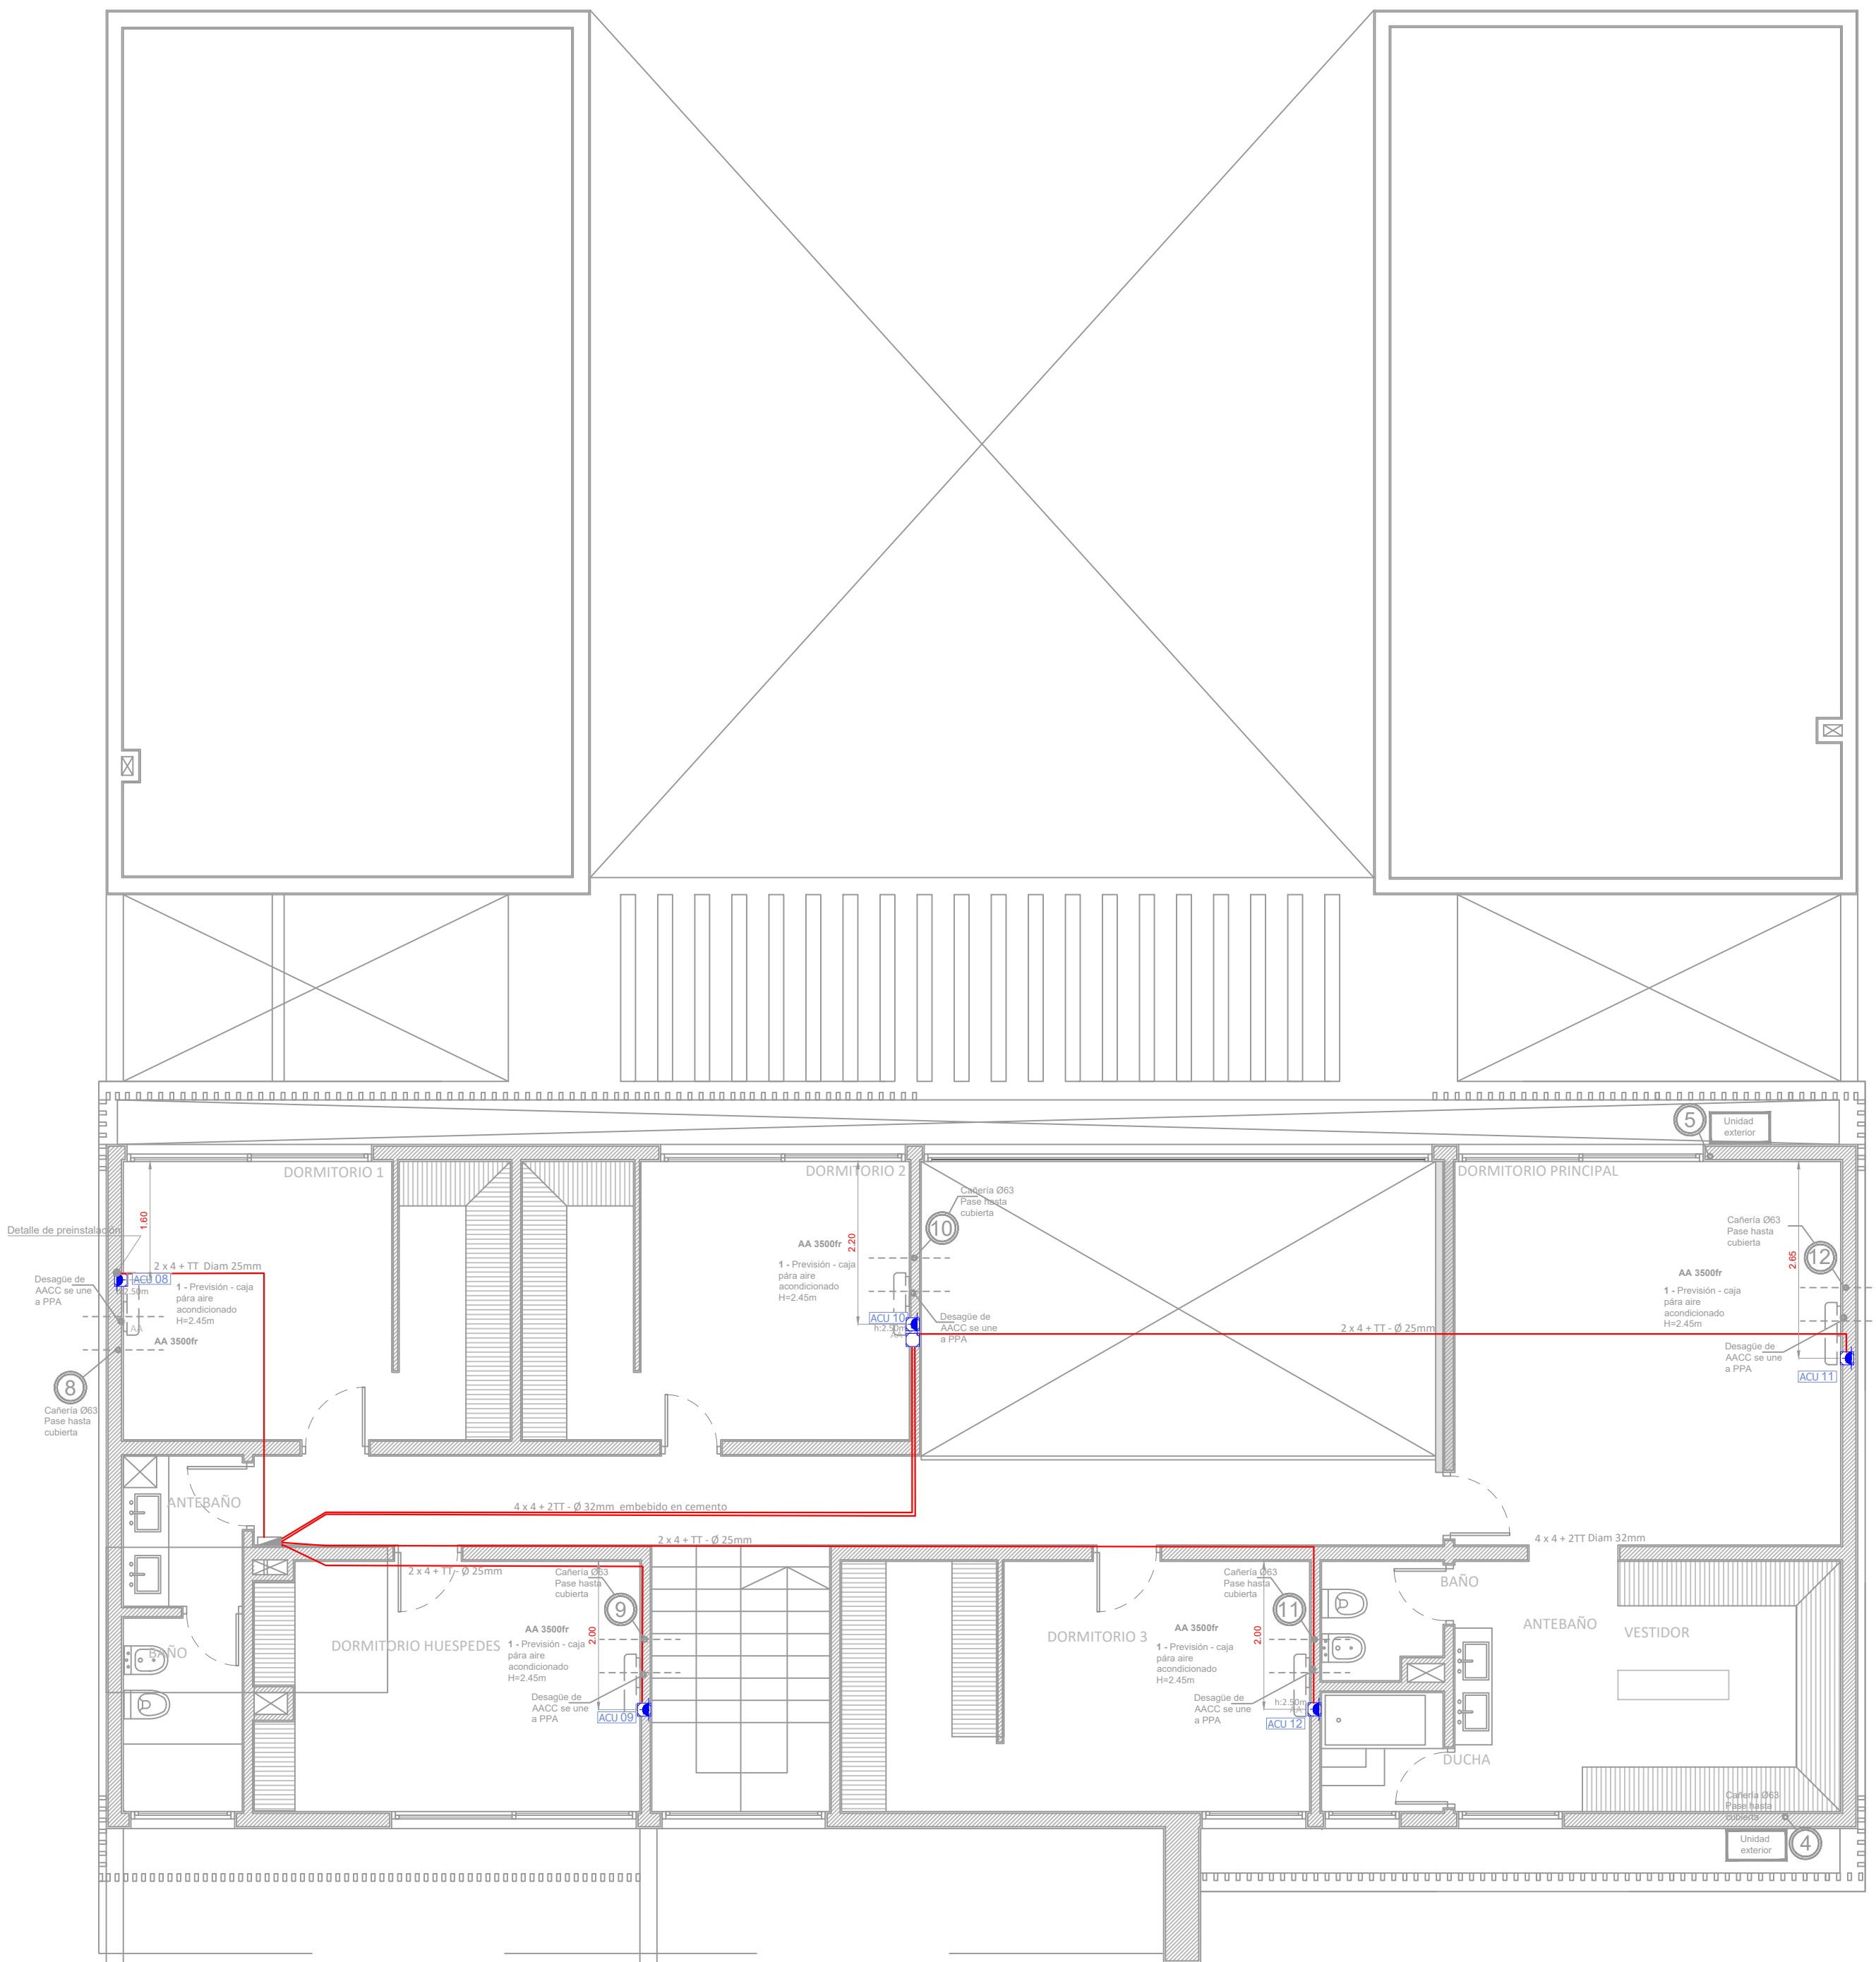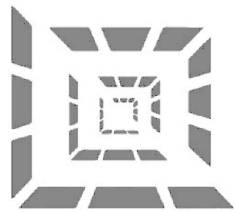

REFERENCIAS

- Equipo de Aire Acondicionado con caja de preinstalación
- Cable #63 para paso de cañerías de AAC hasta techo. Pase en vigas
- Desagüe caño 1" conectado a Pileta de Pato de sistema cloacal

DETALLES DE CAJAS DE PREINSTALACIÓN

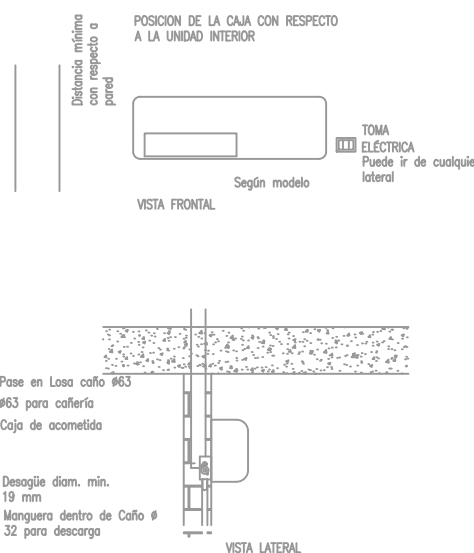

REFERENCIAS ELECTRICIDAD

	Toma Simple 10A
	Toma doble 10A
	Toma doble 10A capsulado
	Extractor de aire
	Caja estanca 10x10
	Toma Simple 20A
	Motor cortienro