

DEL FONDO AL S.U.M.

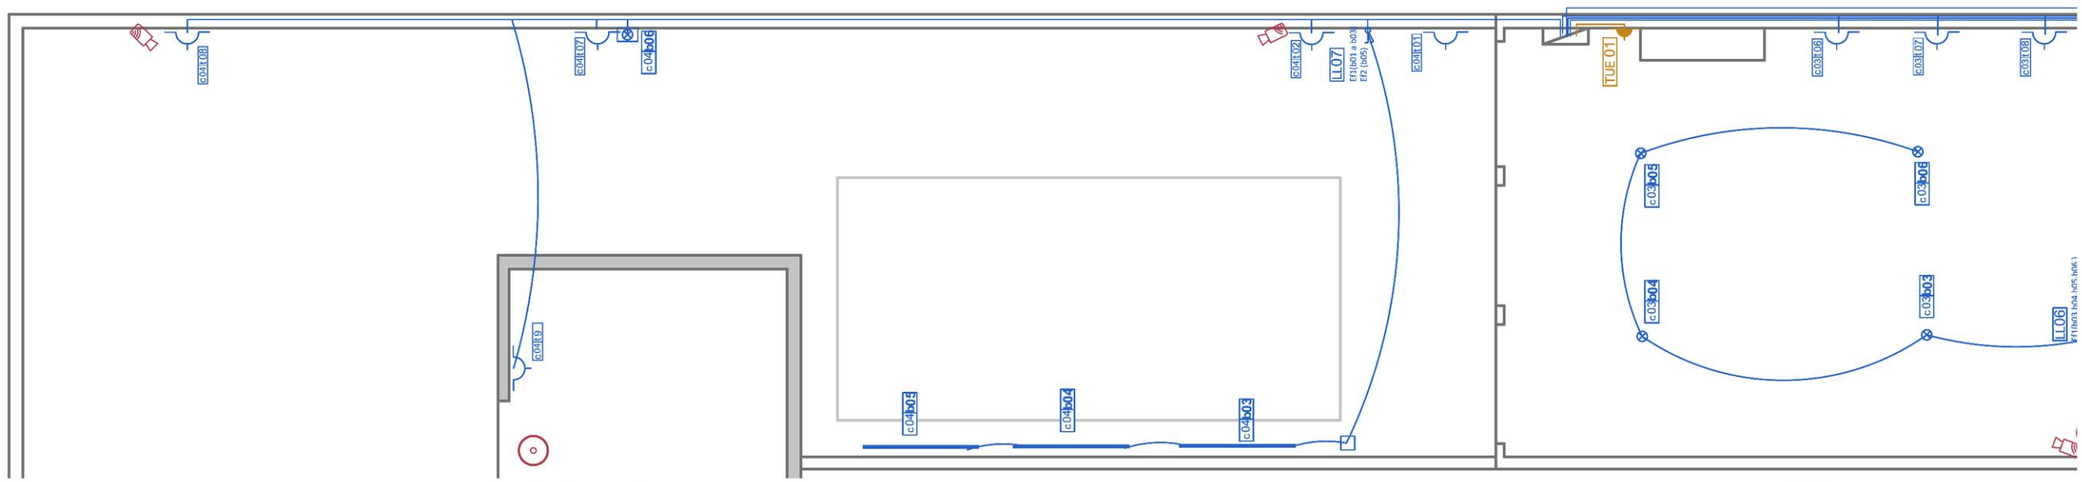

DEL TEMPLO AL INGRESO

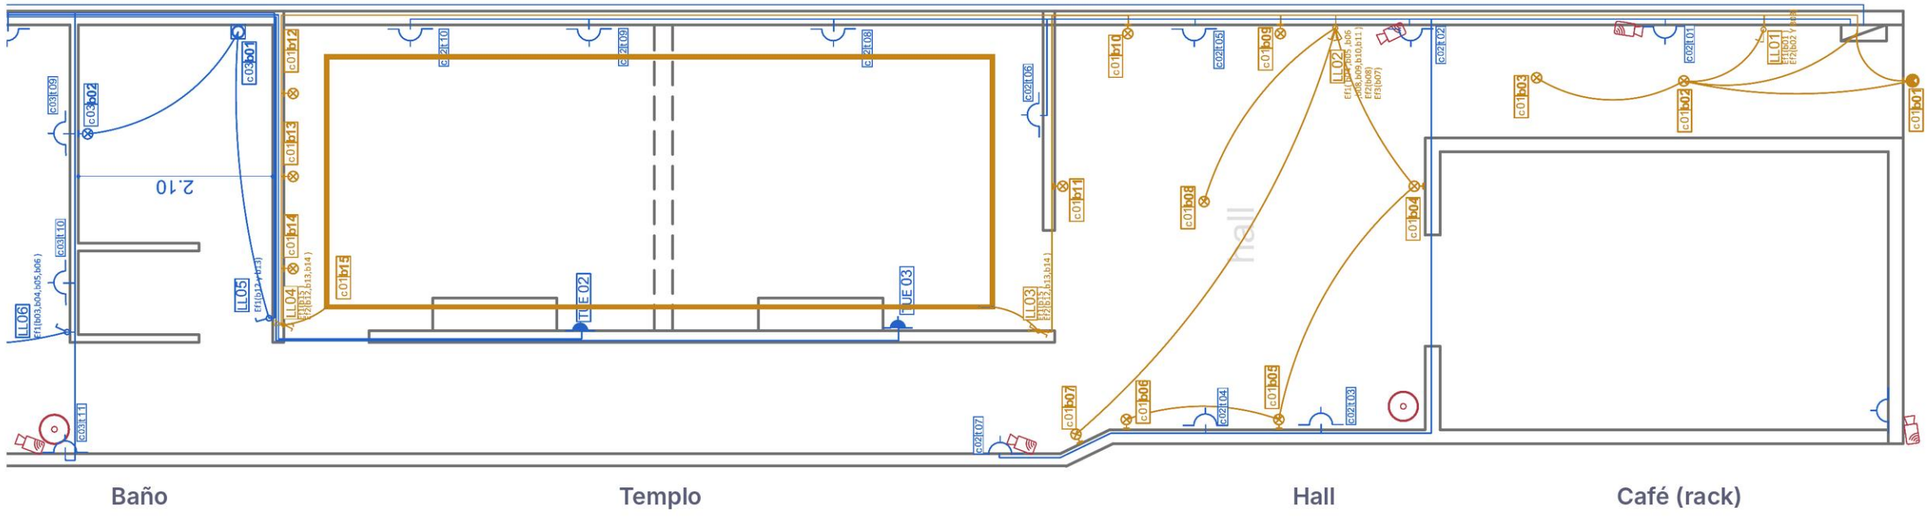

A cargo de Musso (propiedad)

- Bocas existentes que se recanalizan y recablean: 10 de luz, 3 llaves, 22 tomas y 2 tomas especiales
- Tableros principal y secundario, puesta a tierra y troncal entre tableros (línea superior)
- Incluye el S.U.M., el baño, el patio y las tomas del frente

A cargo de la Masonería — electricidad

- Bocas nuevas: 15 de luz (hall, ingreso y templo), 4 llaves y la toma especial TUE01
- La tira LED del templo (rectángulo) se define con la luminotecnia
- Certificado de instalación apta de toda la casona

A cargo de la Masonería — cámaras y red

- 7 cámaras y 3 access point: la canalización va en la Parte 2 y los equipos en la Parte 3
- Rack, grabador y router en el café, donde entra internet

Los locales del fondo, sin bocas dibujadas, mantienen su instalación y se conectan a la nueva. Los rótulos de cada boca (c01 b05, LL03, TUE02…) son los del plano eléctrico original.