


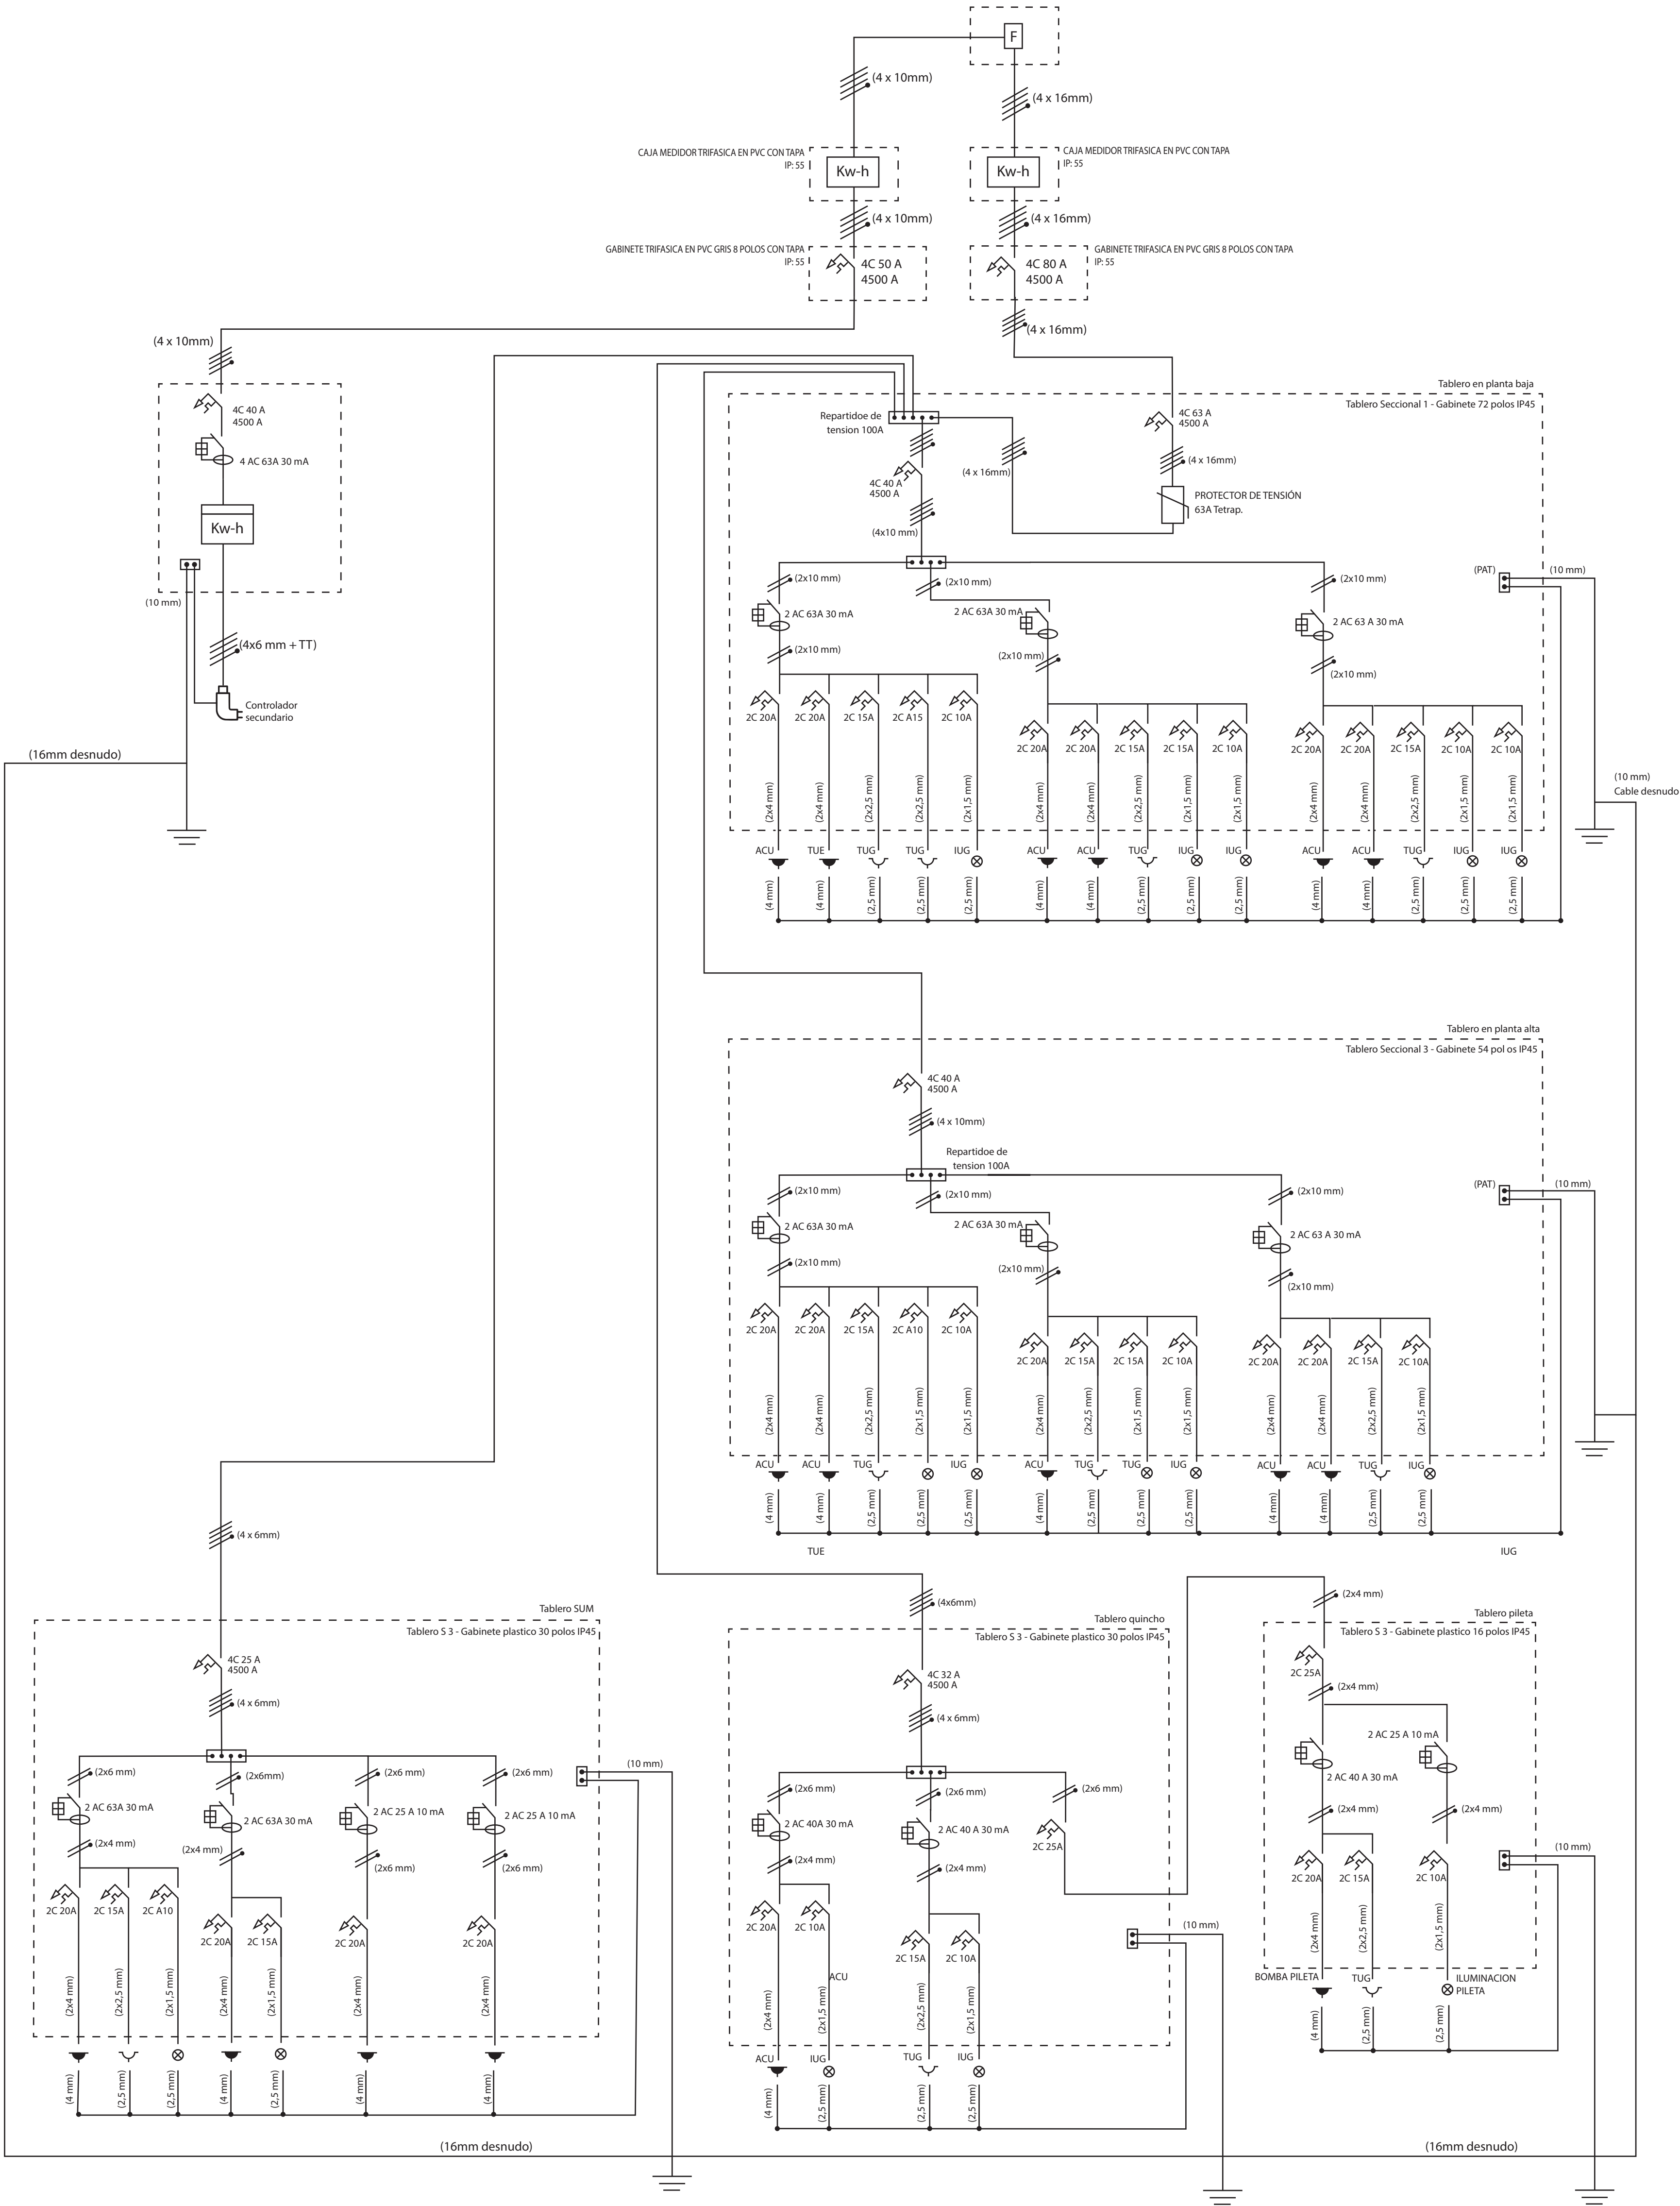


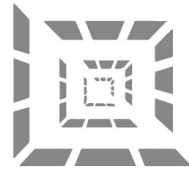

Estudio jad - Casa JB - Campos del virrey

PLANTA BAJA - TABLEROS + TT

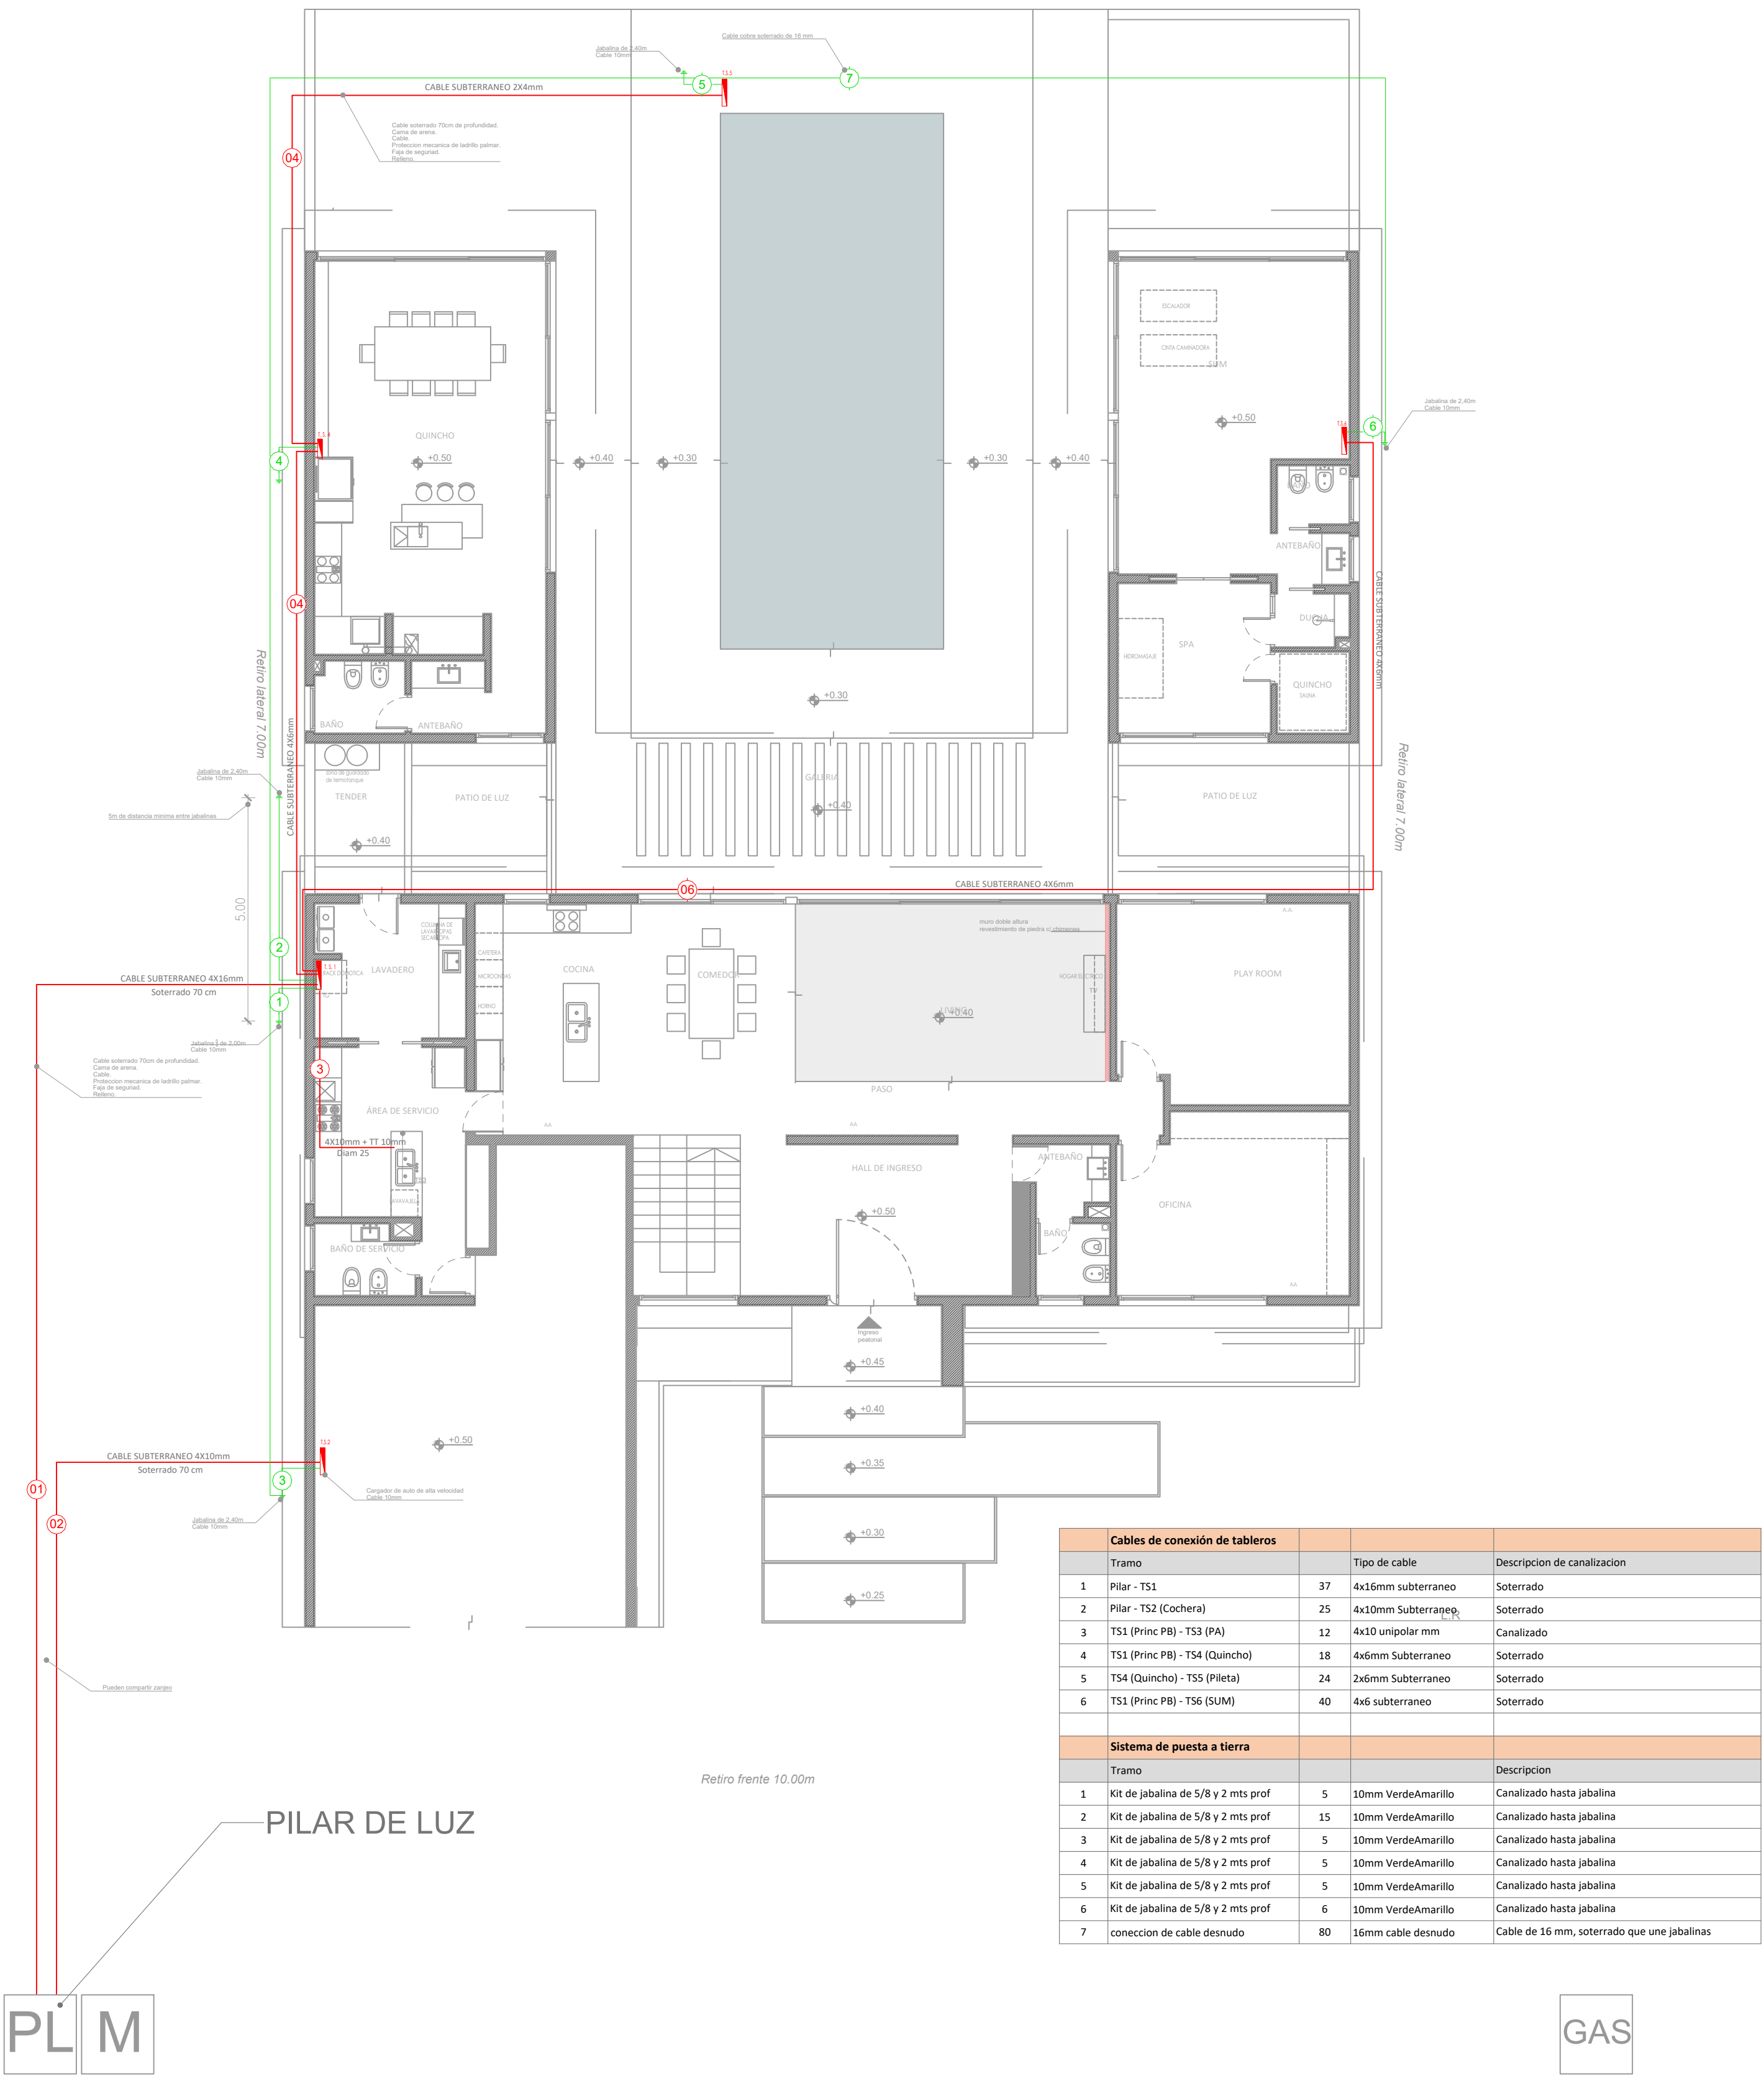

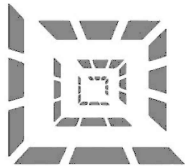

Estudio jad - Casa JB - Campos del virrey

PLANTA ALTA - TABLEROS + TT

