



Estudio jad - Casa JB - Campos del virrey

PLANTA BAJA - SEALES DEBILES

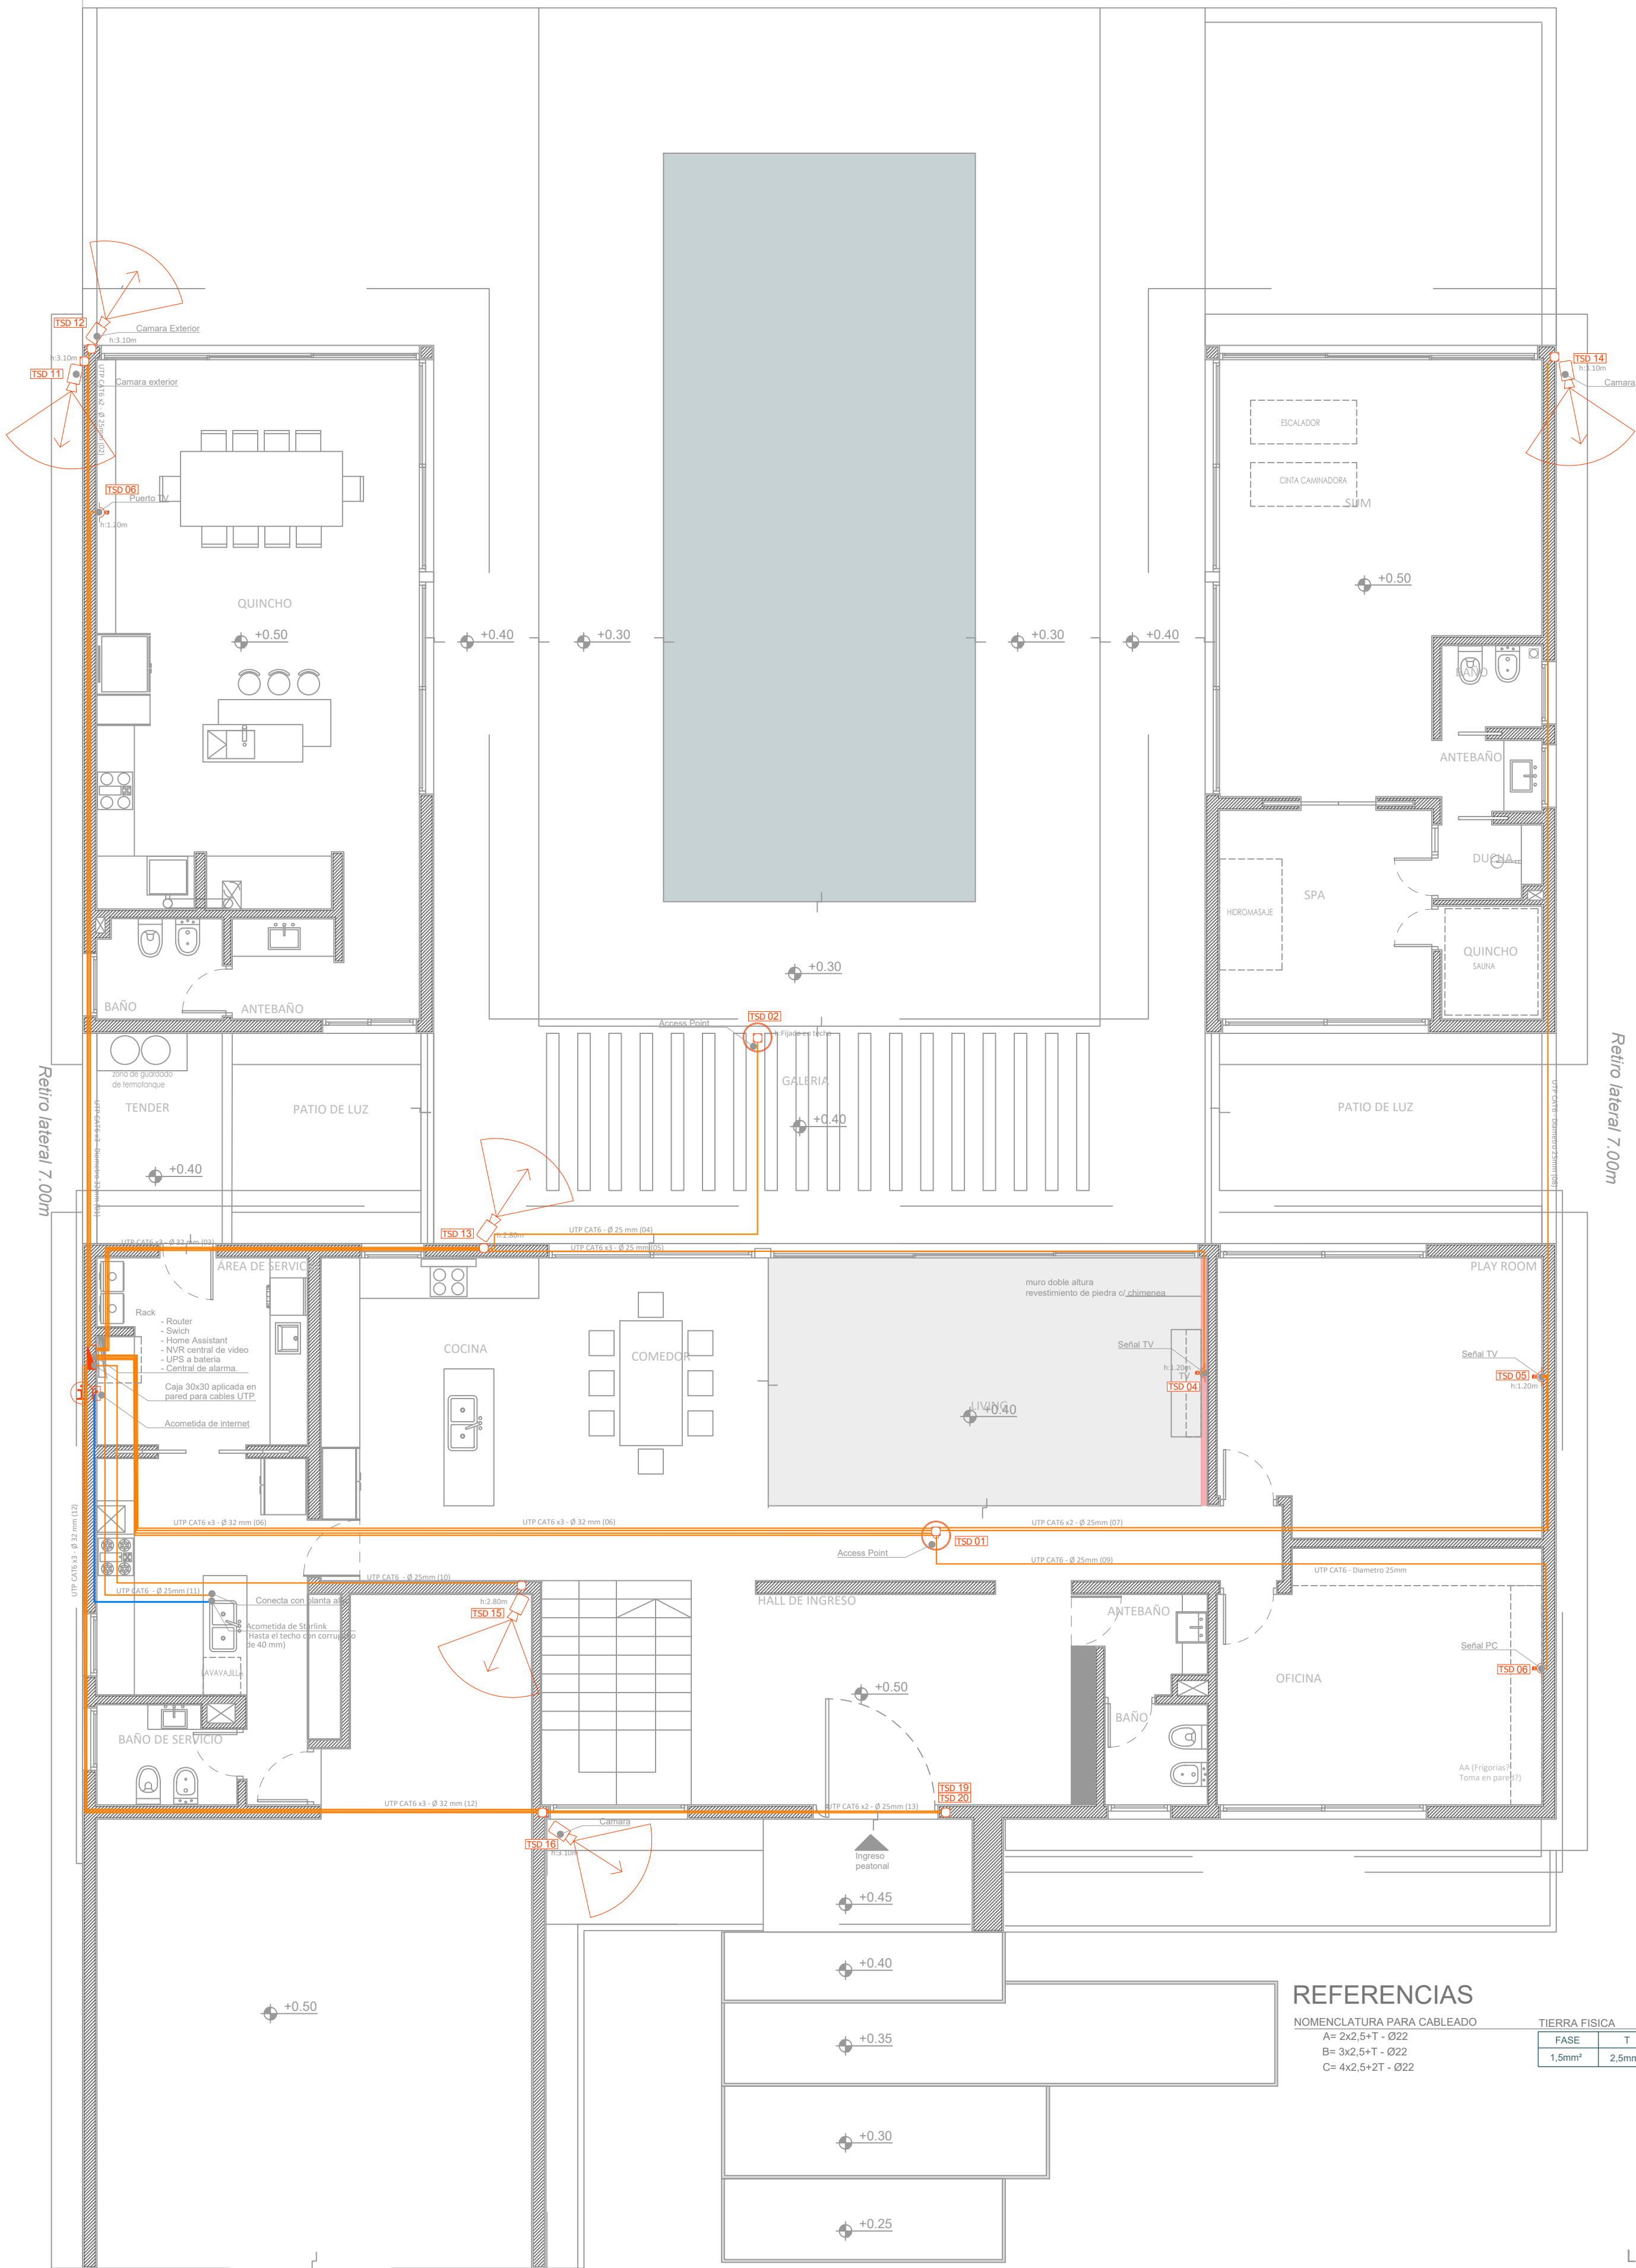

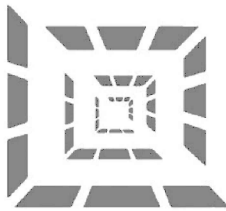

	Acometida de internet
	Modem
	Rack
	Dispositivo Shelly
	Caja estanca rectangular
	Caja estanca cuadrada
	Access Point
	Camara UTP
	Camara inalambrica
	Caja aplicada con UTP-Cat6 RJ45
	ROSETA (Hembra de) RJ45
	
	Angulo de vision de las camaras